

# DARTANK

D É C O R A T I O N   A R C H I T E C T U R A L E

## MAGASIN-SHOWROOM PREMIUM

DOSSIER D'AMÉNAGEMENT — 200 m<sup>2</sup>

PLAN · FAÇADE · PODIUMS · ROOM SETS · ÉCLAIRAGE · MATÉRIAUX · SIGNALÉTIQUE

en collaboration avec MAISON DRAPÉE — papiers peints

CONCEPT & PLANCHES

|    |                                    |       |
|----|------------------------------------|-------|
| 01 | Plan d'aménagement 2D + parcours   | p. 3  |
| 02 | Façade + vitrine                   | p. 4  |
| 03 | Showroom produits — podiums        | p. 5  |
| 04 | Murs (room sets) + matériauthèque  | p. 6  |
| 05 | Vue perspective 1                  | p. 7  |
| 06 | Concept d'éclairage scénographique | p. 8  |
| 07 | Mood board matériaux & finitions   | p. 9  |
| 08 | Signalétique, vitrine & logo       | p. 10 |

DÉTAILS TECHNIQUES

|    |                                   |       |
|----|-----------------------------------|-------|
| 09 | Plan coté — dimensions            | p. 11 |
| 10 | Détail podium modulaire           | p. 12 |
| 11 | Nomenclature des finitions        | p. 13 |
| 12 | Vue perspective 2 (vitrine, jour) | p. 14 |
| 13 | Budget indicatif par poste        | p. 15 |

EN BREF

- 200 m² · 9 zones · parcours guidé
- Sélection curatée + matériauthèque + catalogue
- Podiums & room sets modulaires, renouvelables
- Éclairage scénographique, 4 scénarios
- Anthracite #1A1A1A + bronze #9C7A4D


Budget indicatif ≈ 178–281 k€ HT

# DARTANK

MAGASIN-SHOWROOM — PLAN D'AMÉNAGEMENT 2D

SÉLECTION CURATÉE · PARCOURS GUIDÉ

≈ 200 m<sup>2</sup> (12 × 17 m) · éch. ≈ 1:65 · cotes en m

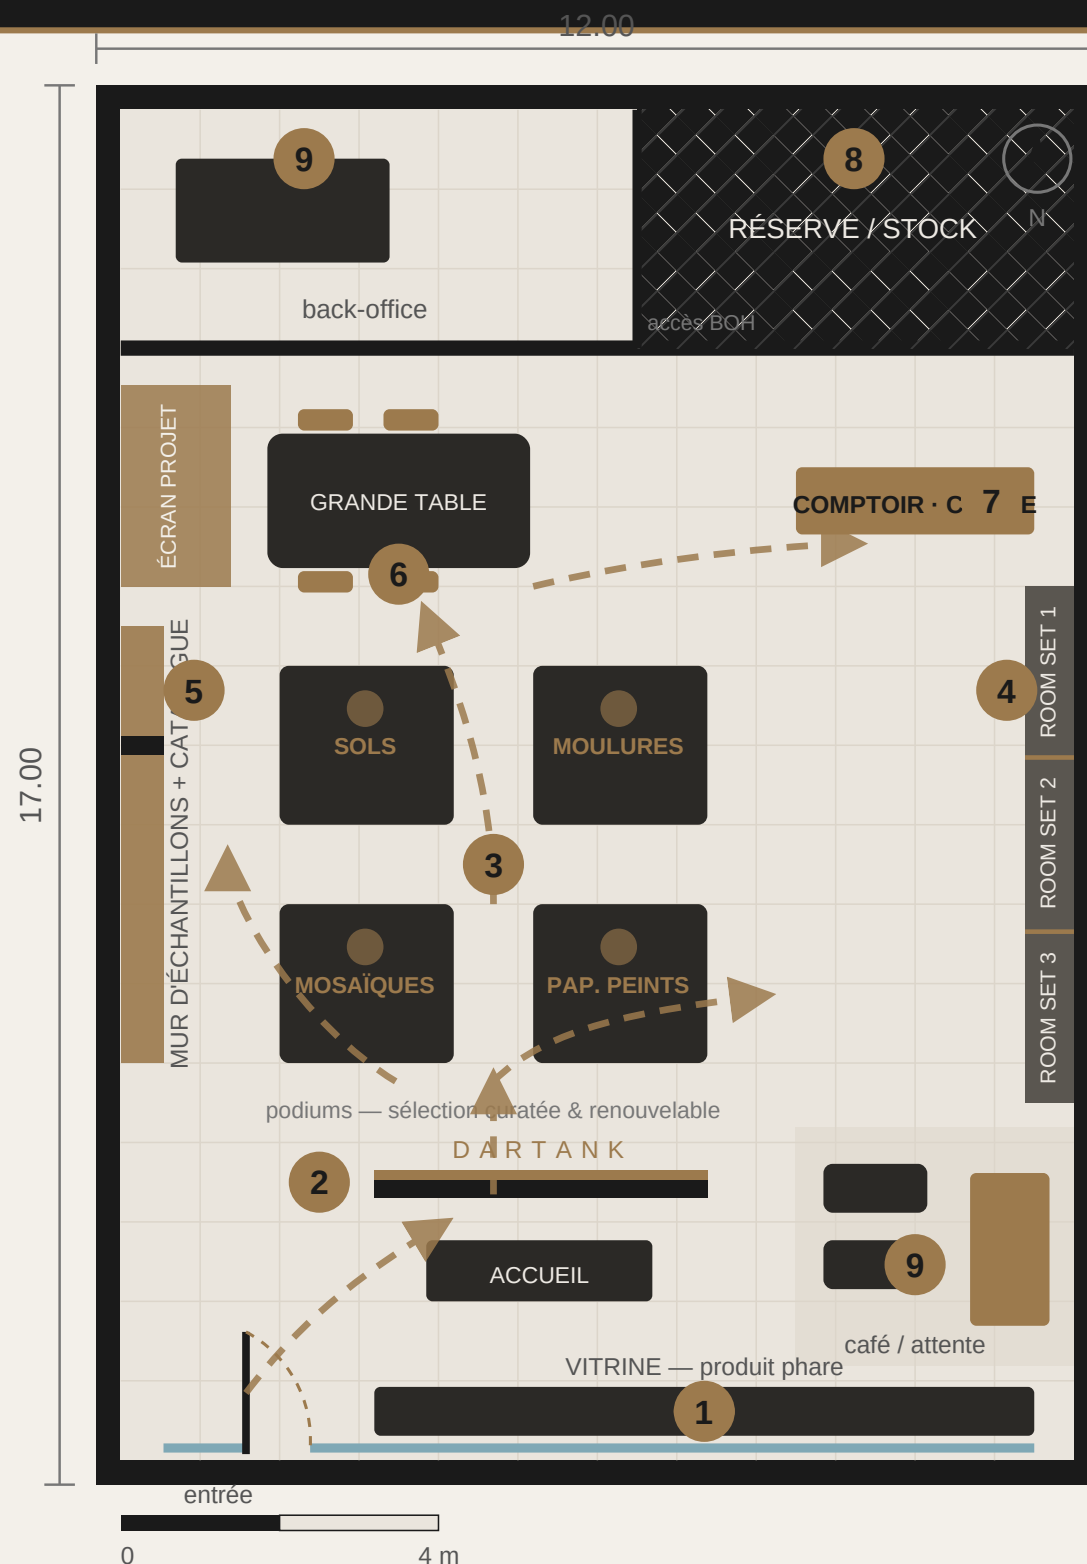


## PROGRAMME

- 1 Façade · enseigne · vitrine**  
Produit phare mis en scène
  - 2 Accueil + mur signature**  
Logo · matière · lumière
  - 3 Showroom produits (podiums)**  
Univers curatés & renouvelables
  - 4 Ambiances scénarisées x3**  
Room sets en situation réelle
  - 5 Matériauthèque + catalogue digital**  
Accès au reste de la gamme
  - 6 Prescription / consultation**  
Grande table · écran · nuanciers
  - 7 Comptoir de vente + caisse**
  - 8 Réserve / stock**  
Gammes à rotation rapide
  - 9 Back-office + café / attente**  
Recevoir & patienter confortablement
- — — — — Parcours client guidé

□ Le magasin expose une sélection curatée ; le reste de la gamme est accessible via la matériauthèque + le catalogue digital (commande sur projet).

## PALETTE

 

Anthracite #1A1A1A



Bronze #9C7A4D



Pierre #EAE5DD

## SURFACES INDICATIVES

|                                   |                     |                            |                     |
|-----------------------------------|---------------------|----------------------------|---------------------|
| Showroom produits + podiums       | ≈ 55 m <sup>2</sup> | Café / attente             | ≈ 14 m <sup>2</sup> |
| Ambiances scénarisées (room sets) | ≈ 28 m <sup>2</sup> | Matériauthèque + catalogue | ≈ 12 m <sup>2</sup> |
| Accueil + signature + vitrine     | ≈ 24 m <sup>2</sup> | Back-office                | ≈ 12 m <sup>2</sup> |
| Prescription / consultation       | ≈ 18 m <sup>2</sup> | Comptoir + caisse          | ≈ 11 m <sup>2</sup> |
| Réserve / stock                   | ≈ 18 m <sup>2</sup> | Circulation                | ≈ 8 m <sup>2</sup>  |

## TOTAL

≈ 200 m<sup>2</sup>

Présentoirs modulables · podiums renouvelables · rails d'éclairage évolutifs

DARTANK · Maison Drapée — Magasin-showroom 200 m<sup>2</sup> — Vue d'ensemble (itération 0)

# DARTANK

FAÇADE + VITRINE — ÉLÉVATION


ENSEIGNE & MISE EN SCÈNE PRODUIT PHARE

L 12.00 × H 4.00 m · éch. ≈ 1:60



vitrine — produit phare mis en scène (renouvelable)


## VUE DE NUIT — ENSEIGNE & VITRINE RÉTROÉCLAIRÉES

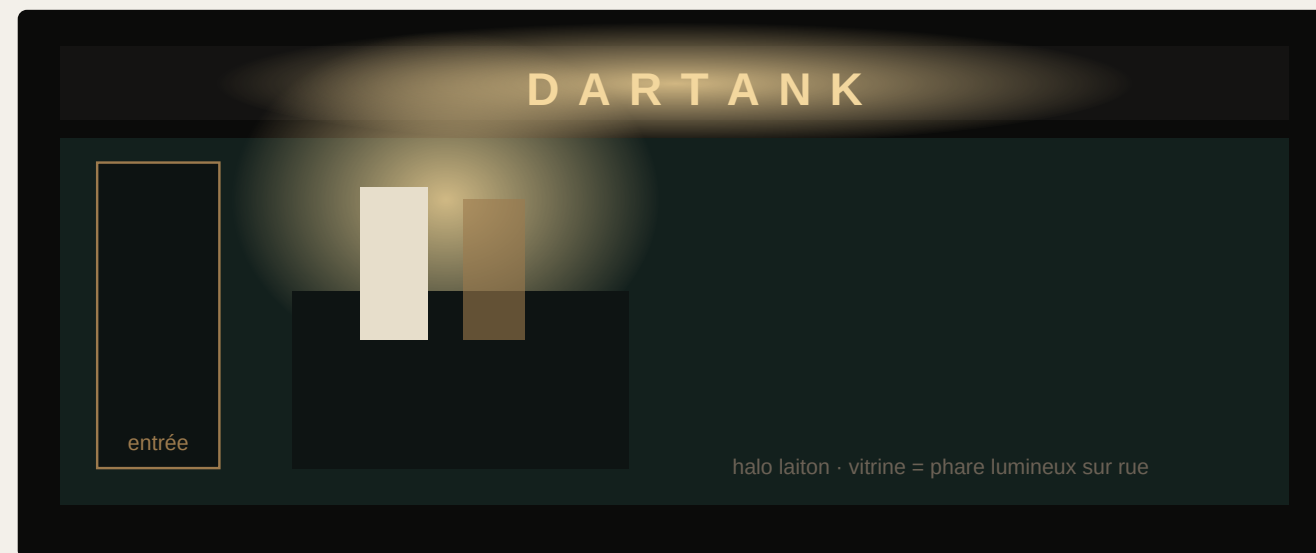

## PRINCIPE & MATIÈRES

- Enseigne : lettres boîtier laiton brossé + emblème, halo LED 3000K
- Vitrine plein cintre : un seul produit phare scénarisé, podium noir mis en lumière — renouvelé à chaque collection / saison
- Châssis anthracite mat, montants fins, verre extra-clair
- Pylône latéral anthracite avec logotype vertical (repère de loin)
- Entrée vitrée à gauche, poignée bâton laiton

**Objectif : lisibilité premium jour & nuit, vitrine = aimant sur rue.**

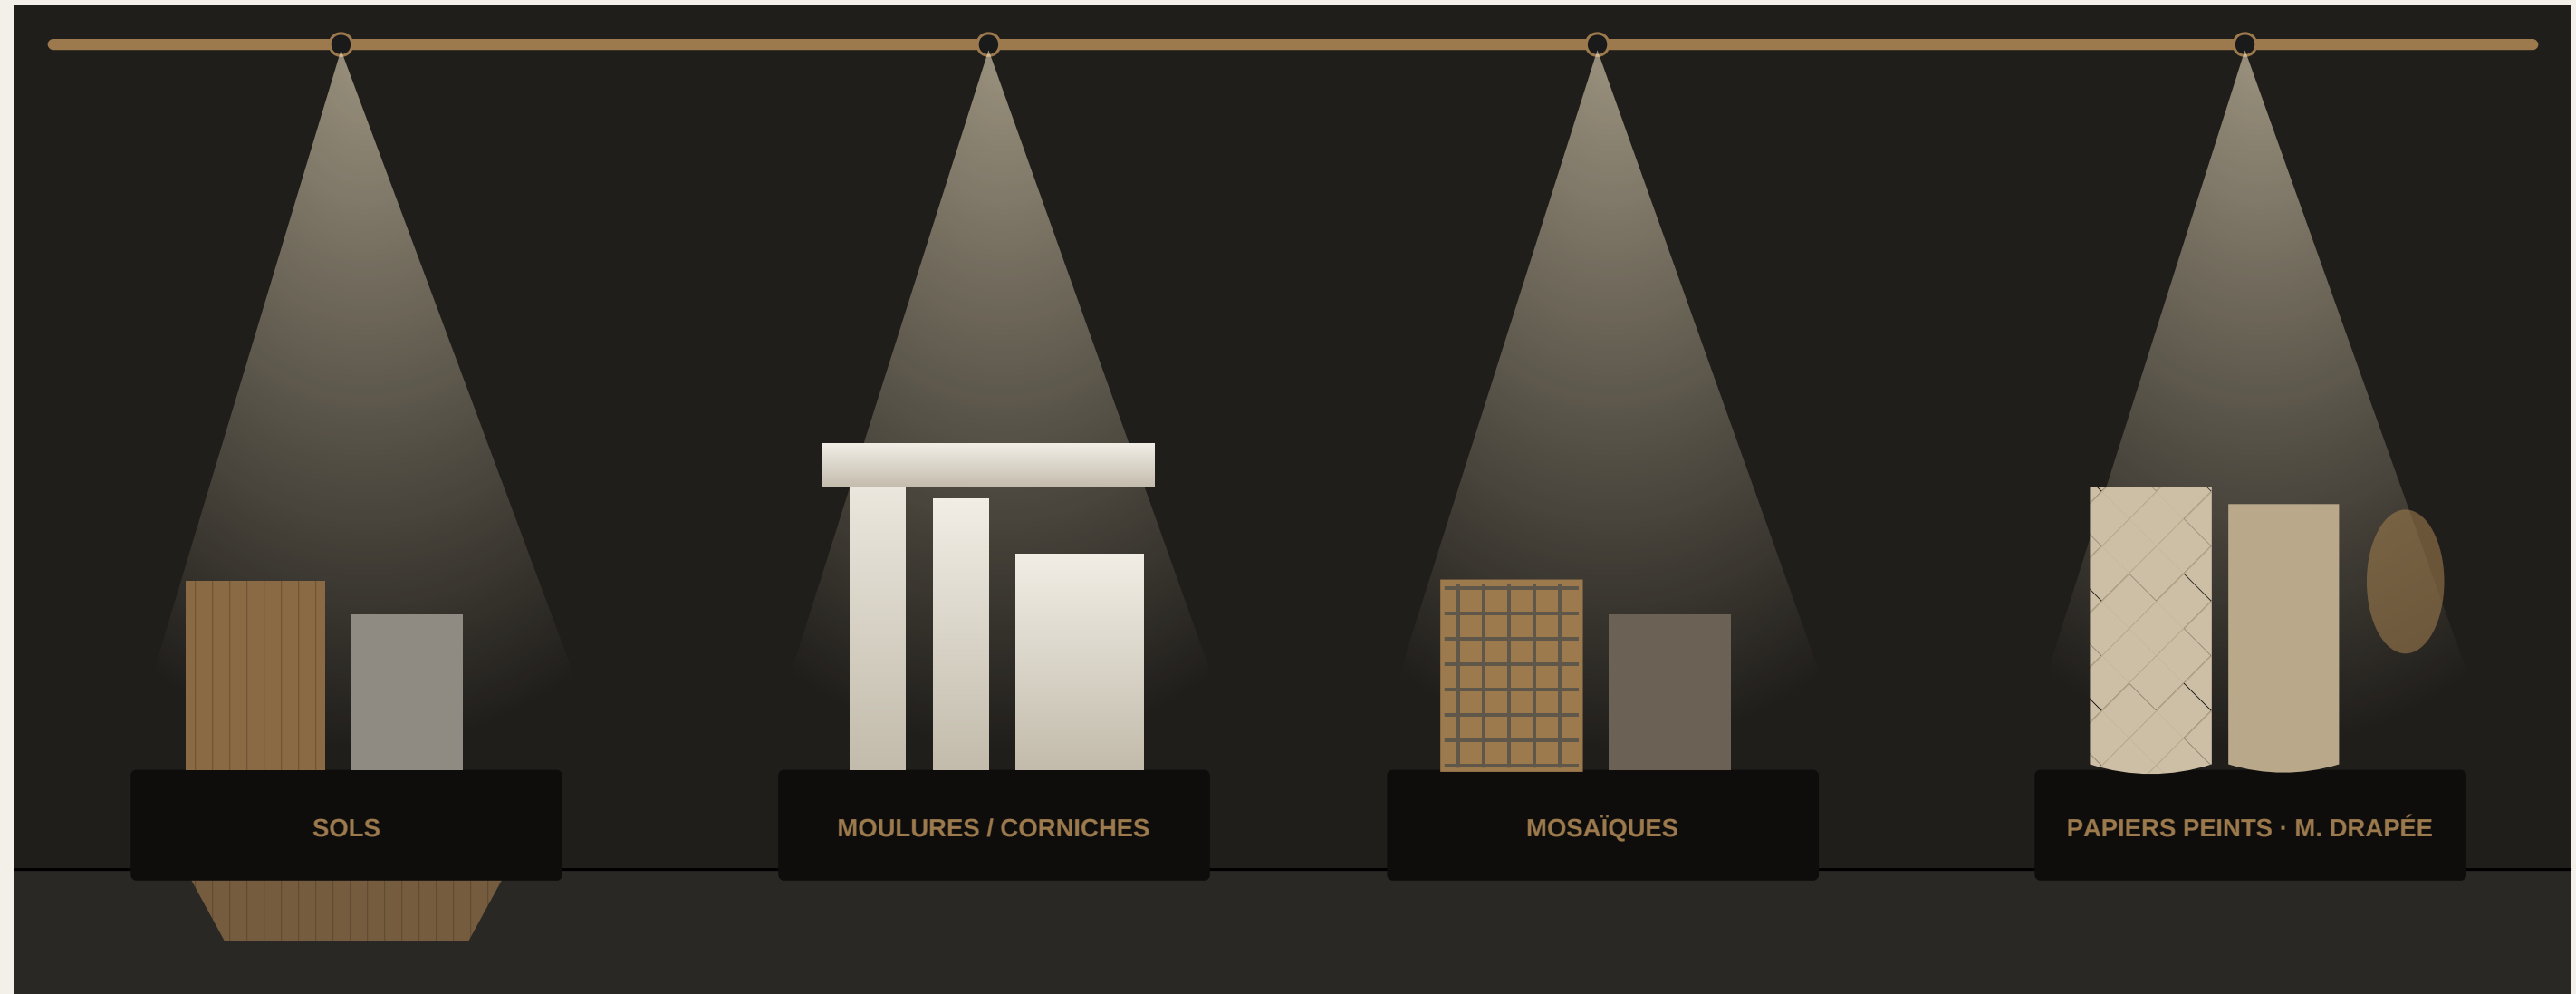


## SYSTÈME DE PRÉSENTATION

- Podiums noirs mats sur fond anthracite — produit isolé, mis en lumière
- 1 podium = 1 univers ; rotation/renouvellement à chaque collection
- Présentoirs modulables : stands inclinés (sols), bras (moulures), cadres (mosaïques), barres + lest (papiers peints)
- Échantillon "à toucher" + plaquette bronze (réf. + QR catalogue)

**Curaté, pas exhaustif — le reste via la matériauthèque (zone 5).**


## IMPLANTATION (rappel plan)

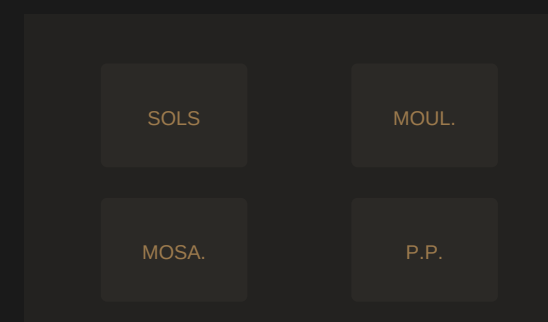


4 podiums au cœur du magasin,  
circulation périphérique fluide,  
vues plongeantes depuis l'entrée.

Espacement ≥ 1.2 m entre podiums  
(confort & accessibilité PMR).

## MUR EST — 3 AMBIANCES SCÉNARISÉES (ROOM SETS)

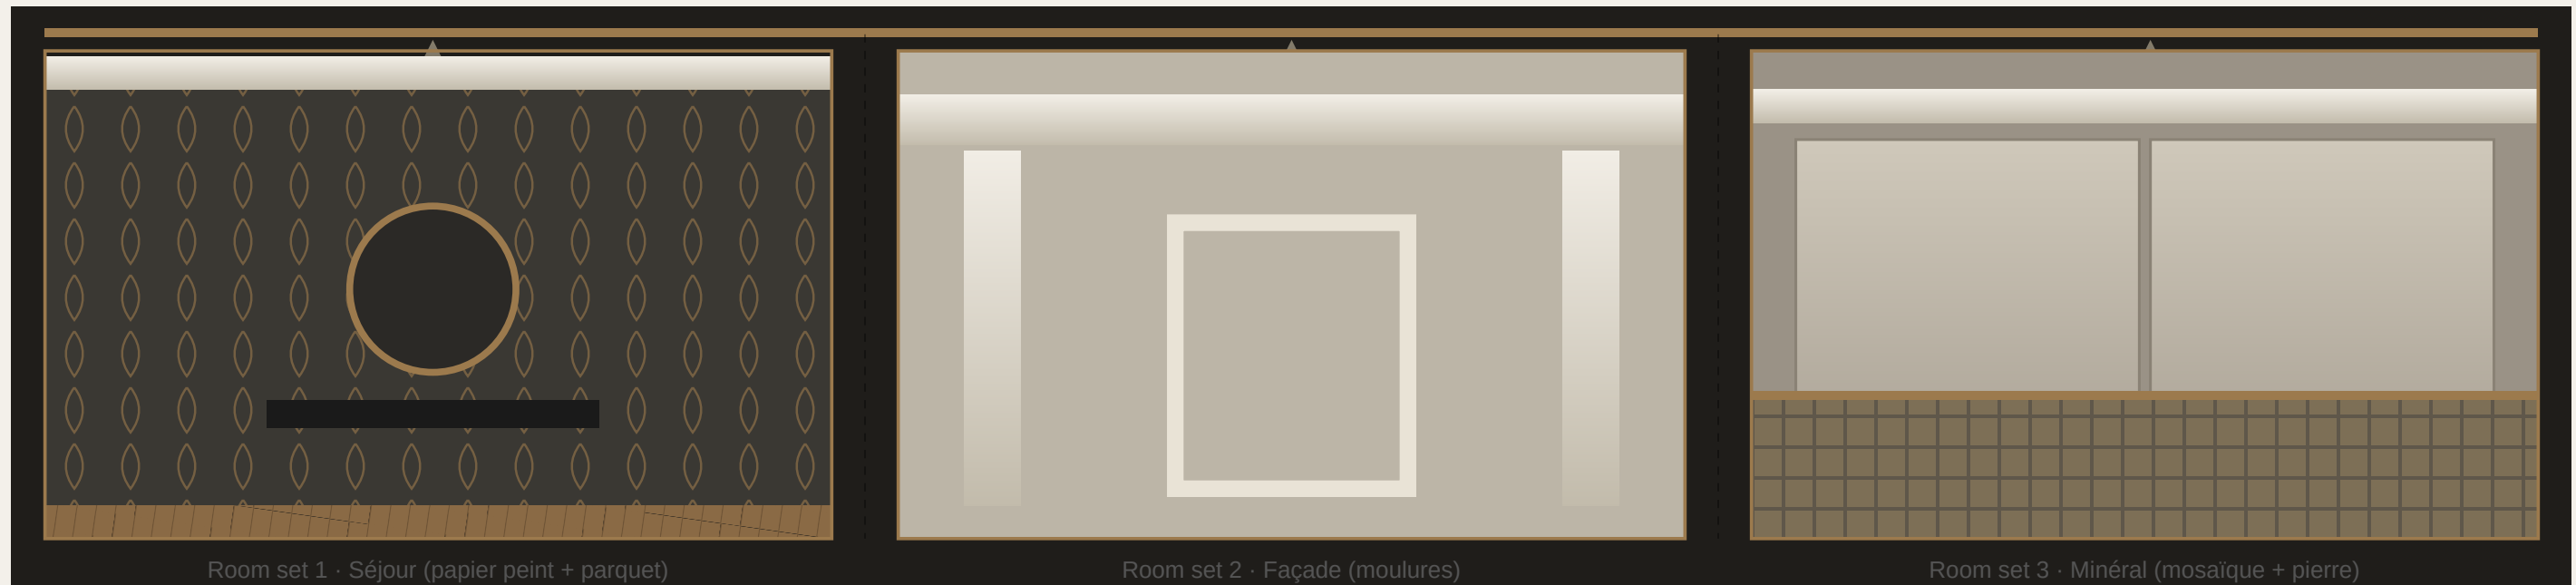

## MUR OUEST — MATÉRIAUTHÈQUE (RESTE DE LA GAMME) + ÉCRAN CATALOGUE DIGITAL

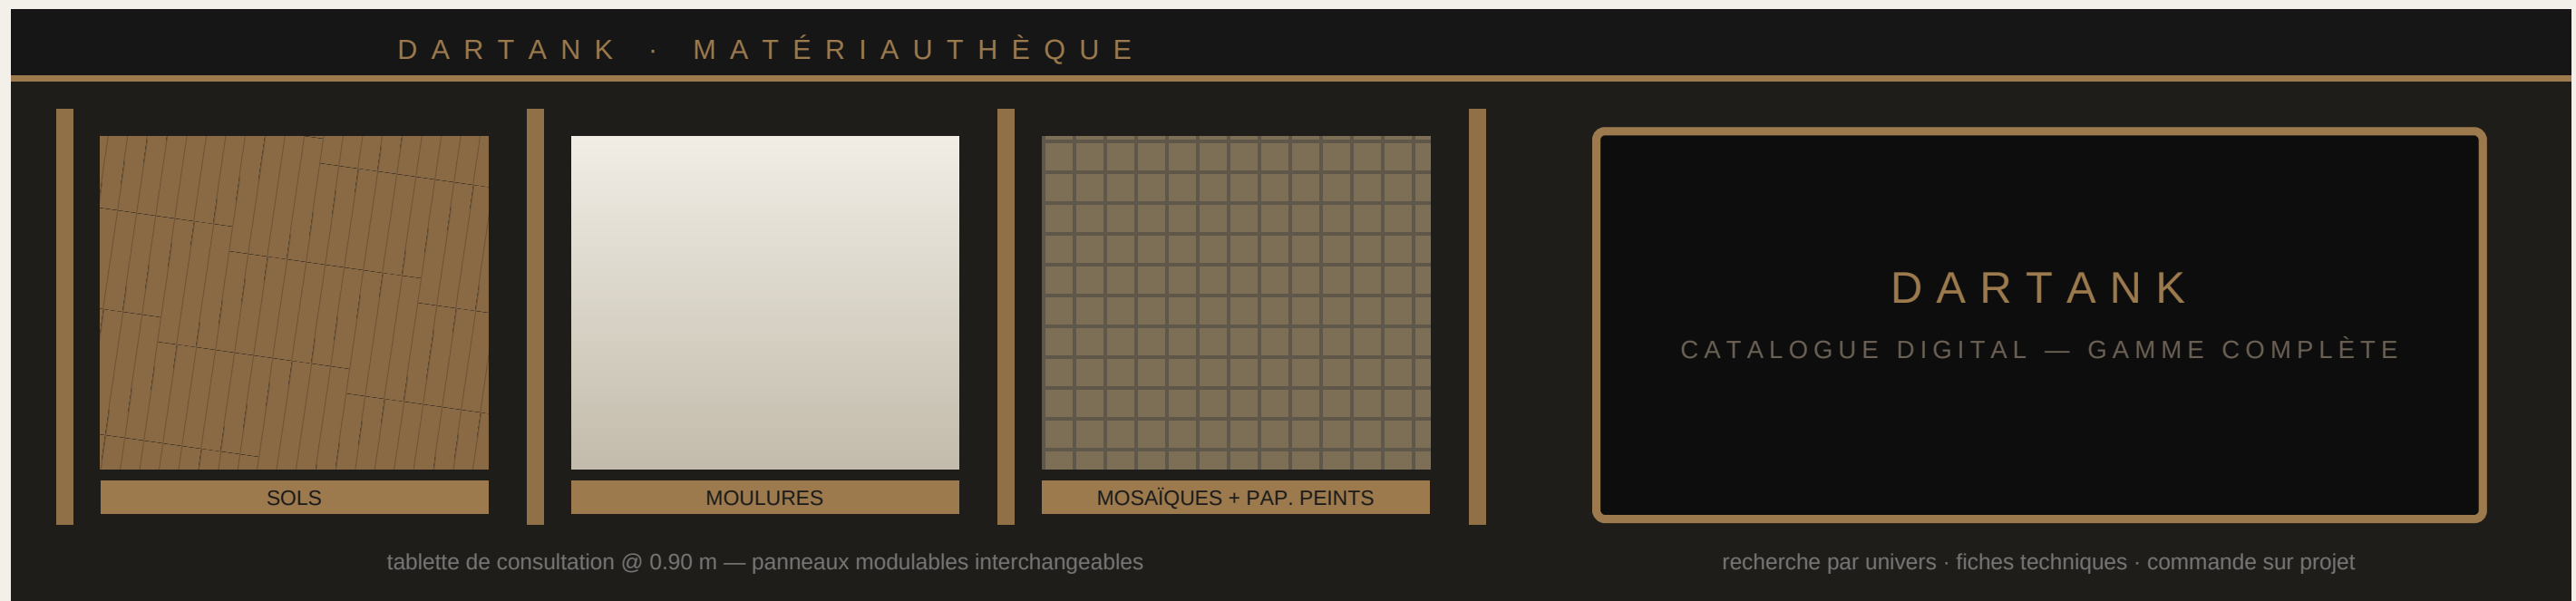

Le mur d'échantillons + l'écran donnent accès à TOUTE la gamme non exposée — sans surcharger le magasin.



# DARTANK

MAGASIN — VUE PERSPECTIVE

DEPUIS L'ENTRÉE VERS LE MUR SIGNATURE

podiums & room sets sous éclairage scénographique




DARTANK · Maison Drapée — Magasin 200 m<sup>2</sup> — Perspective — iteration 1

**Centre** — Podiums produits par univers, isolés & mis en lumière

**Gauche** — Matériauthèque (reste de la gamme) + tablette de consultation

**Droite** — Room sets : papier peint Maison Drapée, moulures de façade

**Fond** — Mur signature rétroéclairé + accueil ; rails de spots scénographiques

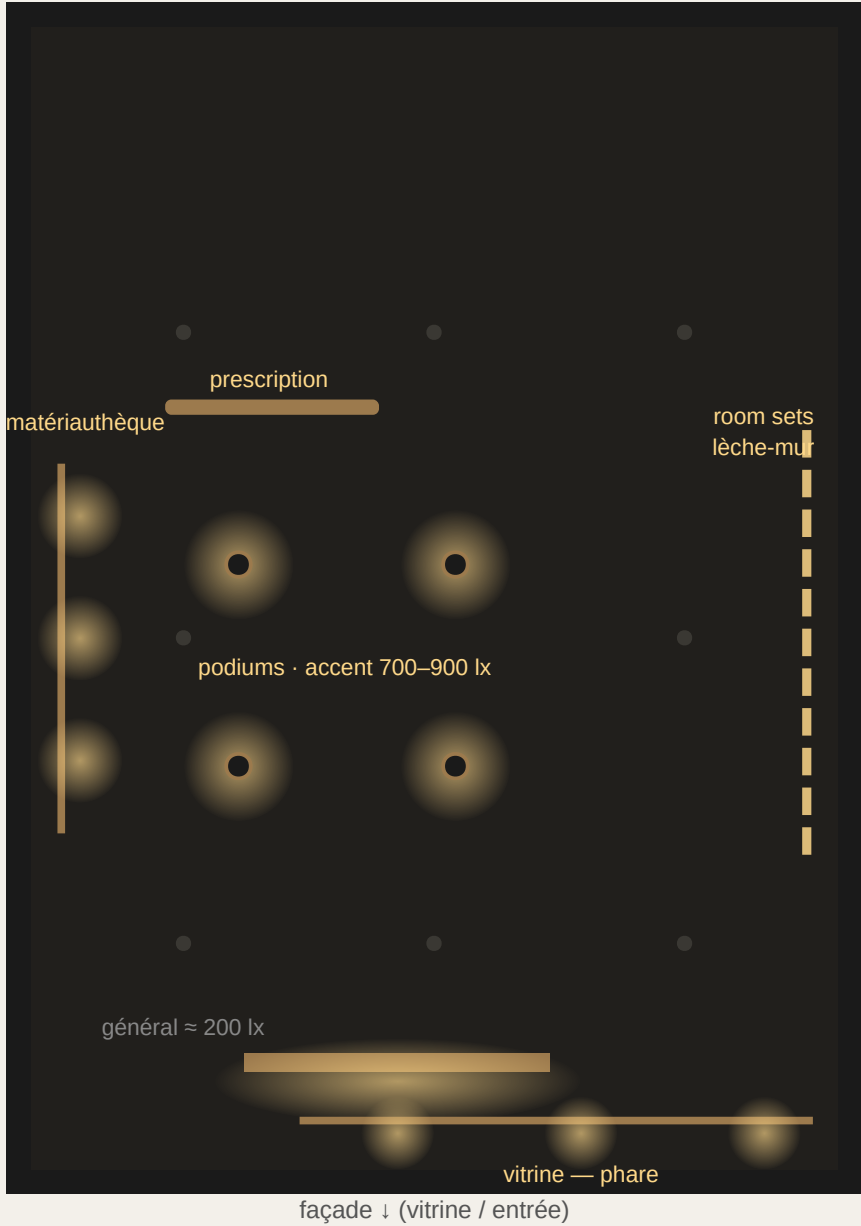

APPAREILS & PARAMÈTRES

- Spot accent sur rail — podiums & vitrine, faisceau serré 15–24°
- Lèche-mur (wall-grazing) — room sets & matériauthèque
- Downlight général encastré — circulation & confort
- Suspension linéaire — table de prescription & accueil

|                          |             |                 |            |
|--------------------------|-------------|-----------------|------------|
| Température              | 2700–3000 K | Accent podiums  | 700–900 lx |
| Rendu couleurs (matière) | IRC > 90    | Room sets       | 500–700 lx |
| Général / circulation    | 200 lx      | Vitrine (phare) | 1000 lx    |

Rails alimentés sur tout le plafond : ajout/déplacement de spots sans travaux — l'éclairage suit le renouvellement des podiums & des room sets.

SCÉNARIOS (gradation DALI)

1 · JOUR COMMERÇANT

Général 100% · accents podiums 80% · vitrine 100% — accueillant & lisible

2 · PRESCRIPTION (pros)

Table 500 lx · accents 100% · matériauthèque renforcée — comparaison fidèle

3 · SOIRÉE / ÉVÉNEMENT

Général 30% · accents + lèche-mur 100% · signature & vitrine — atmosphère

4 · VITRINE NUIT

Enseigne + vitrine produit phare + 1 room set allumés — présence sur rue 24/7

□ Pilotage centralisé, scénarios mémorisés, horloge astronomique pour la vitrine.

Mise en lumière = outil de merchandising : on dirige le regard vers le produit phare.




# DARTANK

MATÉRIAUX & FINITIONS — MOOD BOARD


PALETTE PREMIUM · LIGNES ÉPURÉES

matériaux nobles · accent bronze/laiton

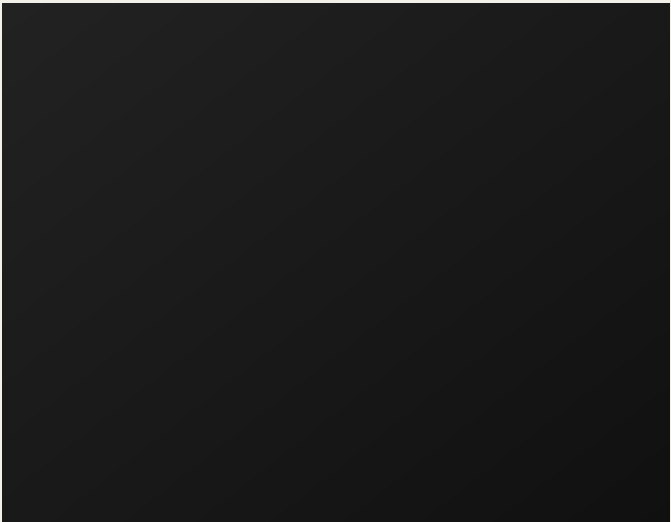

**Anthracite profond** #1A1A1A

Microciment / peinture mate — murs, mobilier, signature

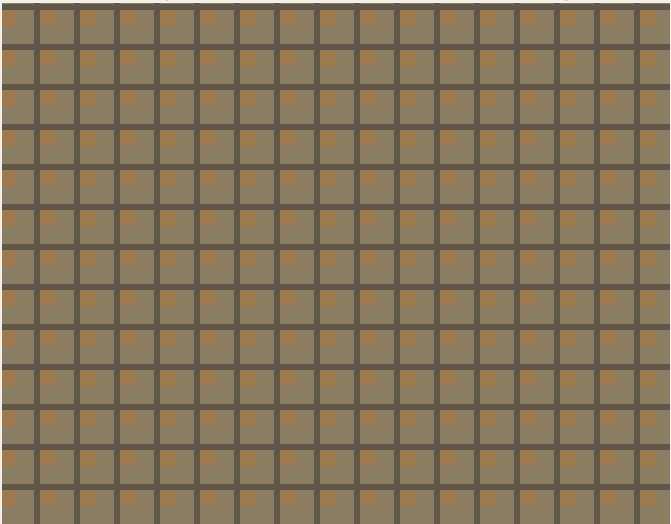

**Mosaïque pierre & or** accent

Touches ponctuelles, soubassements d'ambiance



**Bronze / laiton brossé** #9C7A4D

Détails, lettrage, mains courantes, piétements, rails



**Papier peint Maison Drapée**

Ambiance séjour — lés tendus, textile mural




**Pierre claire** #EAE5DD

Sol showroom, tablettes — respiration claire



**Velours vert profond** #2E3A35

Assise d'appoint / rappel coloré chic

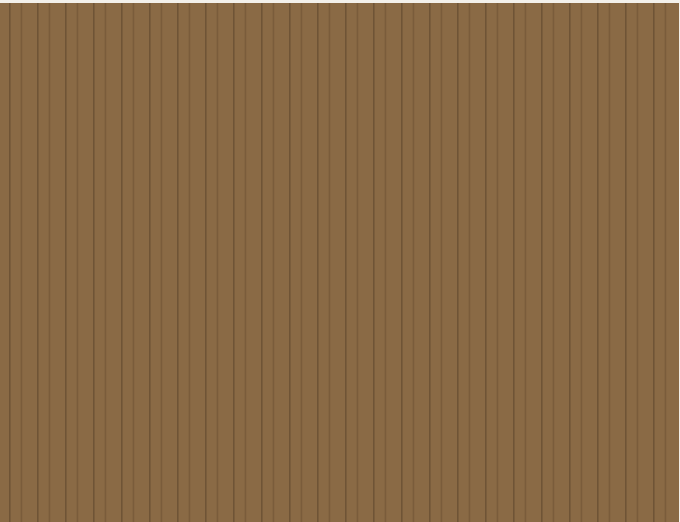

**Chêne fumé** sol / mobilier


Assises, plateau de table, plinthes — chaleur



**Verre & miroir fumé**

Cloisons, vitrine, jeux de reflets & profondeur


## PALETTE

 

Anthracite  
#1A1A1A




Bronze  
#9C7A4D

 

Pierre  
#EAE5DD



Taupe  
#5A5650

 

Vert prof.  
#2E3A35



Chêne  
#8A6A45

## PRINCIPES D'ASSOCIATION

- 80% neutres (anthracite + pierre), 15% bois, 5% bronze en touches — la matière exposée prime.
- Mat contre brillant : fonds mats, accents métalliques brossés & reflets de verre.
- Finitions tactiles — un showroom où l'on touche.


# DARTANK

SIGNALÉTIQUE, VITRINE & LOGO — IDENTITÉ DE MARQUE

ENSEIGNE · VITRINE · MUR SIGNATURE

emblème portail · logotype · endossement

LOGO PRINCIPAL

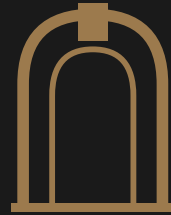

## DARTANK

DÉCORATION ARCHITECTURALE

ENSEIGNE DE FAÇADE — LETTRES BOÎTIER LAITON, RÉTROÉCLAIRAGE HALO



## DARTANK

entrée

MUR D'ACCUEIL — LETTRES BRONZE BROSSÉ + HALO



## DARTANK

DÉCORATION ARCHITECTURALE

— en collaboration avec —  
*Maison Drapée*

VERSION CLAIRE & ENDOSSEMENT



## DARTANK

DÉCORATION ARCHITECTURALE

marque sœur · papiers peints

*Maison Drapée*

PLAQUES DE ZONE — BRONZE SUR ANTHRACITE

01 · SOLS

02 · MOULURES

03 · MOSAÏQUES

04 · PAPIERS P.

**PRESCRIPTION / CONSULTATION**

Plaquettes gravées laiton, fixation aimantée — repositionnables.  
Pictogrammes minimalistes, même langage que l'étiquetage produit.  
Numérotation = renvoi au plan & au catalogue digital.

### TYPOGRAPHIE & CONSTRUCTION

- Logotype : capitales, linéale élégante, interlettrage large (≈ +10%)
  - Emblème "portail" = évocation moulure / façade architecturale
  - Endossement Maison Drapée en italique fin, jamais plus grand que DARTANK
- Zone de protection = hauteur du « D » sur tout le pourtour.

### MATIÈRES & FABRICATION

- Enseigne : lettres boîtier laiton brossé, rétroéclairage halo LED 3000K
  - Mur signature : lettres relief bronze brossé sur fond microciment anthracite
  - Vitrine : logo & mention dépolis / sérigraphiés sur verre, lettrage laiton
- Cohérence façade ↔ vitrine ↔ intérieur ↔ étiquette produit ↔ catalogue digital.


DARTANK · Maison Drapée — Magasin 200 m² — Signalétique, vitrine & logo — itération 1

# DARTANK

PLAN COTÉ — DIMENSIONS INDICATIVES

12.00 × 17.00 m = 204 m²

éch. ≈ 1:65 · cotes en m

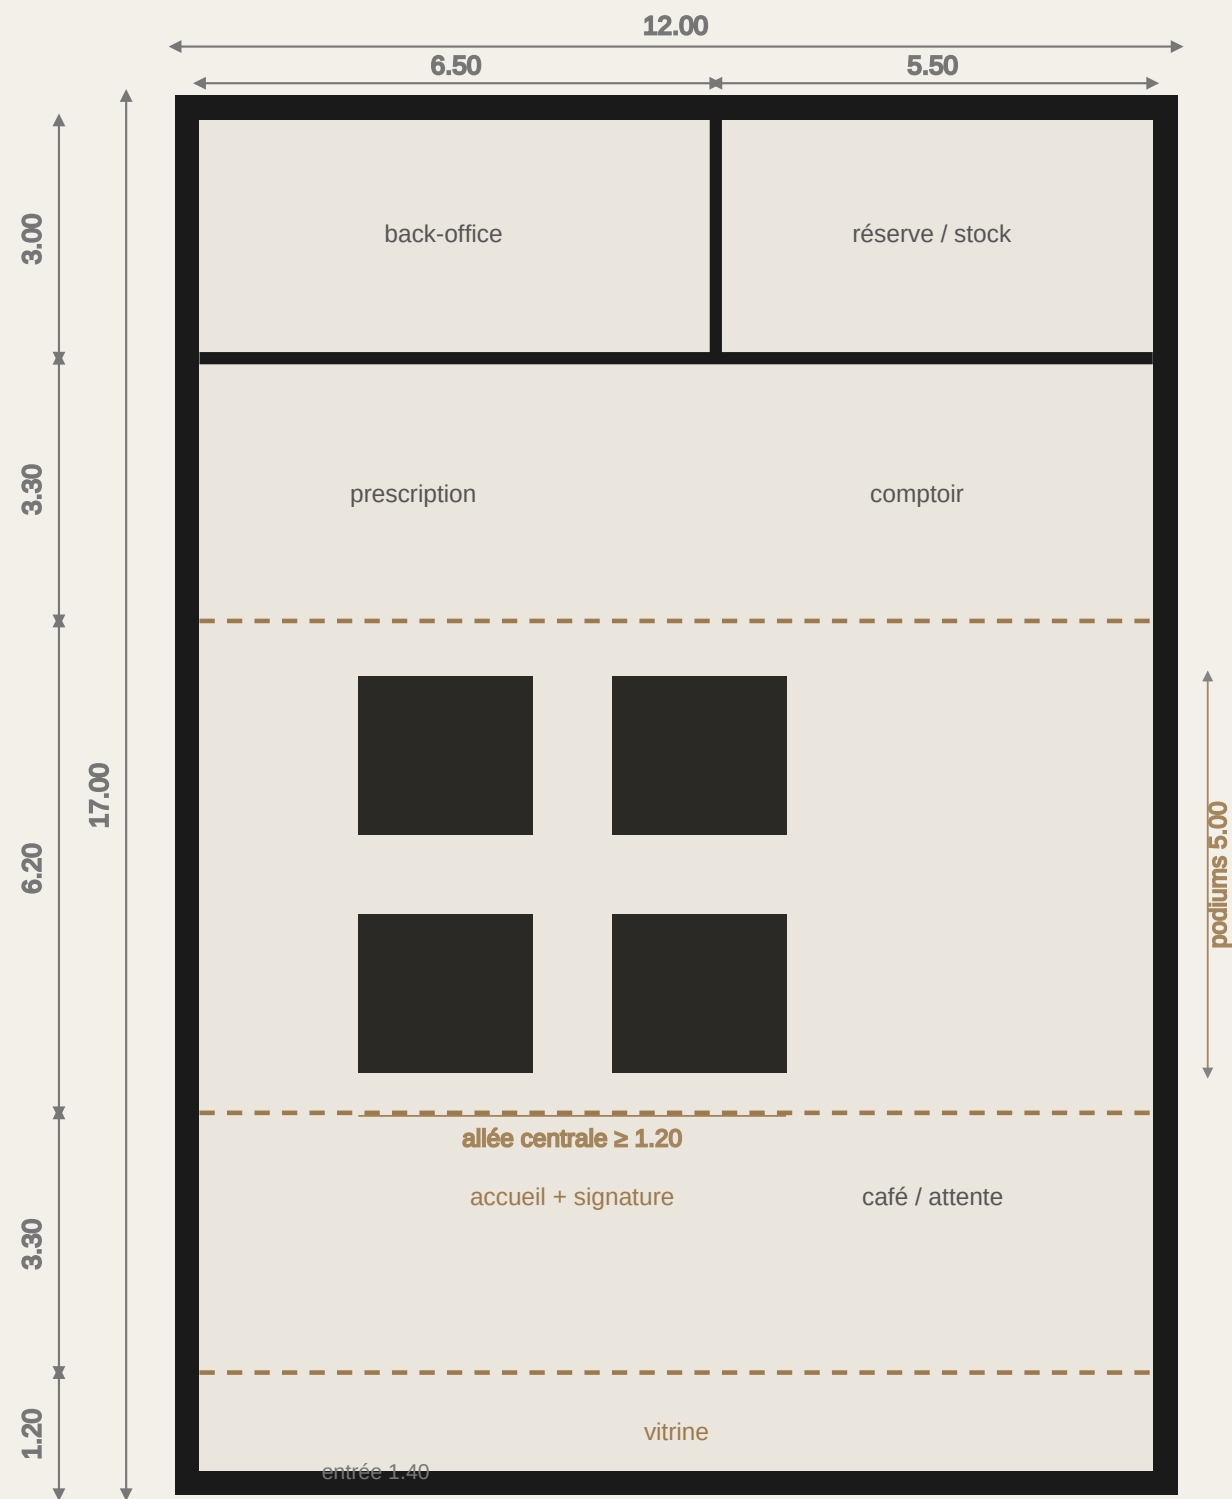

## CLEARANCES & ACCESSIBILITÉ

|                        |          |
|------------------------|----------|
| Allées principales     | ≥ 1.50 m |
| Entre podiums          | ≥ 1.20 m |
| Porte d'entrée (libre) | 1.40 m   |
| Accès réserve / BOH    | 0.90 m   |
| Hauteur sous plafond   | 3.20 m   |
| Aire de rotation PMR   | Ø 1.50 m |

- Toutes cotes indicatives, à relever sur site avant exécution.
- Trame structurale à confirmer (poteaux, réseaux, issues de secours).
- Conformité ERP / accessibilité PMR à valider avec bureau de contrôle.

Surface utile ≈ 204 m² (hors cloisons).

## RÉPARTITION PAR BANDE (profondeur)

|                  |        |                                      |
|------------------|--------|--------------------------------------|
| Bande fond (BOH) | 3.00 m | réserve + back-office                |
| Bande service    | 3.30 m | prescription + comptoir/caisse       |
| Bande showroom   | 6.20 m | podiums + room sets + matériauthèque |
| Bande accueil    | 3.30 m | accueil + signature + café           |
| Bande façade     | 1.20 m | vitrine + entrée                     |

Profondeur totale 17.00 m


# DARTANK

PODIUM MODULAIRE — DÉTAIL DE PRINCIPE

PRÉSENTOIR ÉVOLUTIF & RENOUVELABLE


cotes en m · détail ≈ 1:20

## A · ÉLÉVATION TYPE

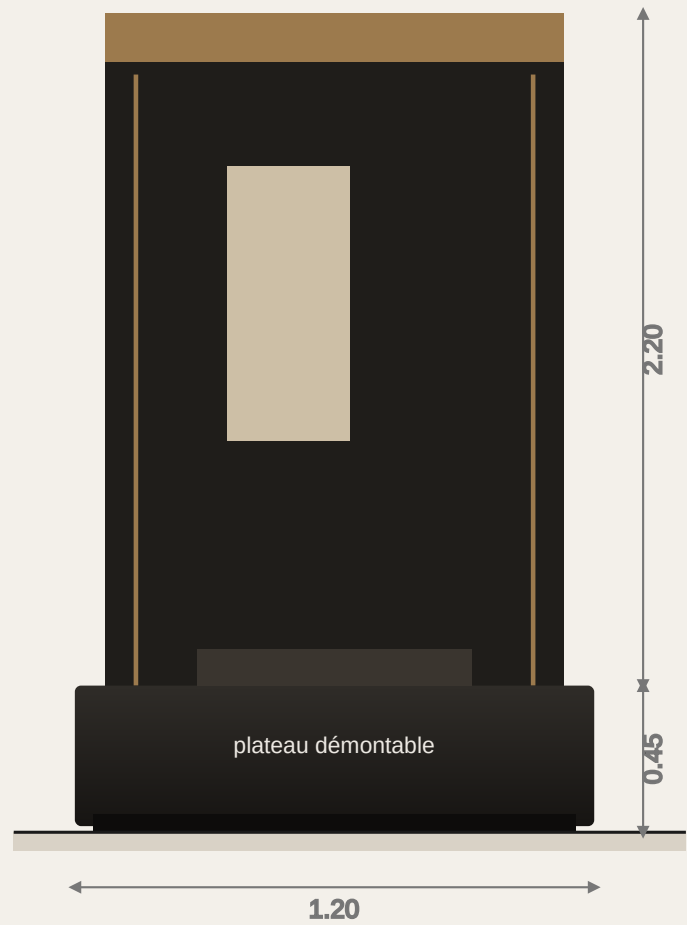

## B · COUPE — CONSTRUCTION

panneau dossier

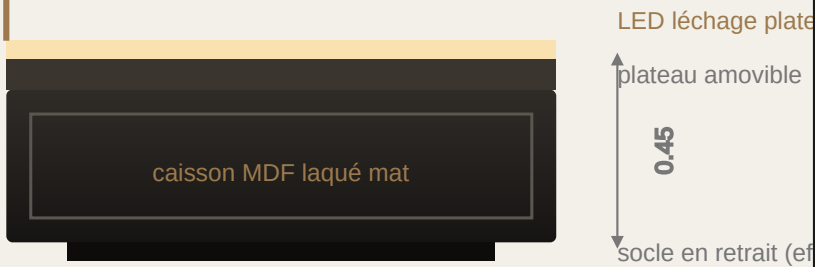

## SPÉCIFICATIONS

|                  |                             |
|------------------|-----------------------------|
| Empreinte socle  | 1.20 × 0.80 m               |
| Hauteur plateau  | 0.45 m                      |
| Panneau dossier  | H 2.20 m                    |
| Caisson          | MDF laqué mat               |
| Plateau          | amovible / interchangeable  |
| Socle            | en retrait (effet flottant) |
| Accroche dossier | rail crémaillère bronze     |
| Éclairage        | spot rail + LED option      |

## MODULARITÉ



- 1 socle commun → 4 kits de présentation
- Changement d'univers = changement de plateau + dossier, sans toucher au socle
- Renouvellement par collection / saison
- Déplaçable (patins) pour réagencer le magasin
- Plaquette bronze réf. + QR → catalogue

## ÉCONOMIE

Investissement concentré sur un socle durable ; les kits (peu coûteux) tournent. Vitrine toujours « neuve » à budget maîtrisé.

Cible : 4 podiums + 2 podiums d'appoint pour temps forts / nouveautés.

## C · VARIANTES DE PRÉSENTOIR (même socle)

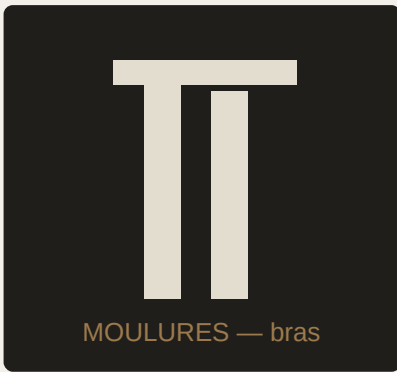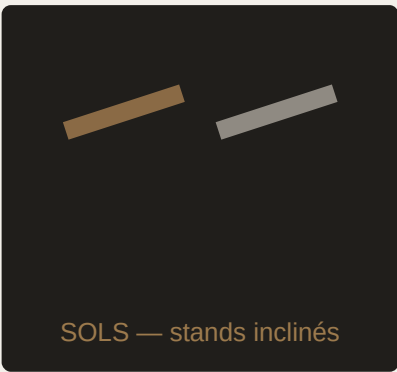

| ZONE                    | SOL                          | MURS / FONDS                             | ÉCLAIRAGE                            | MOBILIER / AGENCEMENT                      |
|-------------------------|------------------------------|------------------------------------------|--------------------------------------|--------------------------------------------|
| 1 · Façade / vitrine    | grand format pierre clr      | châssis anthracite, verre extra-clair    | spots accent 1000 lx + halo enseigne | podium phare noir laqué                    |
| 2 · Accueil + signature | pierre claire mate           | microciment anthracite + logo bronze     | wash mural + suspension accueil      | banque d'accueil laiton/anthracite         |
| 3 · Showroom podiums    | pierre claire / microciment  | anthracite mat (fond podiums)            | spots serrés 700–900 lx / podium     | podiums modulaires MDF laqué               |
| 4 · Room sets (×3)      | parquet / mosaïque selon set | papier peint, moulures, pierre montés    | lèche-mur 500–700 lx                 | décors interchangeableables, cadres bronze |
| 5 · Matériauthèque      | pierre claire                | panneaux modulables / crémaillère bronze | lèche-mur + spots + écran rétroécl.  | tablette 0.90 m, écran catalogue           |
| 6 · Prescription        | parquet chêne fumé           | anthracite + velours vert (acoustique)   | suspension linéaire 500 lx, 3000K    | grande table, écran projet, nuanciers      |
| 7 · Comptoir + caisse   | pierre claire                | parement anthracite + logo bronze        | suspension + accent caisse           | comptoir laiton brossé, back-counter       |
| 8 · Réserve / stock     | résine / béton ciré          | peinture lessivable claire               | réglettes LED fonctionnelles 300 lx  | rayonnages métal, casiers gammes rapides   |
| 9 · Back-office + café  | chêne fumé / pierre          | anthracite + touche velours vert         | général doux 200 lx + liseuses       | bureau, lounge, point café laiton          |

RÉFÉRENCES DE FINITION

- Microciment anthracite mat — murs signature, fonds podiums
- Laiton / bronze brossé — logo, comptoir, rails, détails
- Pierre claire grand format — sol showroom, circulation
- Chêne fumé — parquet prescription, mobilier, plinthes
- Velours vert profond — assises, panneaux acoustiques

Toutes finitions à valider sur échantillons physiques (mock-up recommandé).

PRINCIPES TRANSVERSES

- Fonds mats & sombres = la matière exposée prime (zéro reflet parasite)
- Bronze = fil rouge de marque (5% des surfaces)
- Sol clair continu = respiration & lisibilité
- Éclairage 2700–3000K, IRC>90 partout
- Acoustique traitée en prescription & café
- Tout l'agencement = modulaire & déplaçable


Cohérence avec le showroom 70 m² (même ADN).

# DARTANK

MAGASIN — VUE PERSPECTIVE 2 (VERS LA VITRINE)

AMBIANCE JOUR · LUMIÈRE NATURELLE

depuis le fond du magasin vers la rue

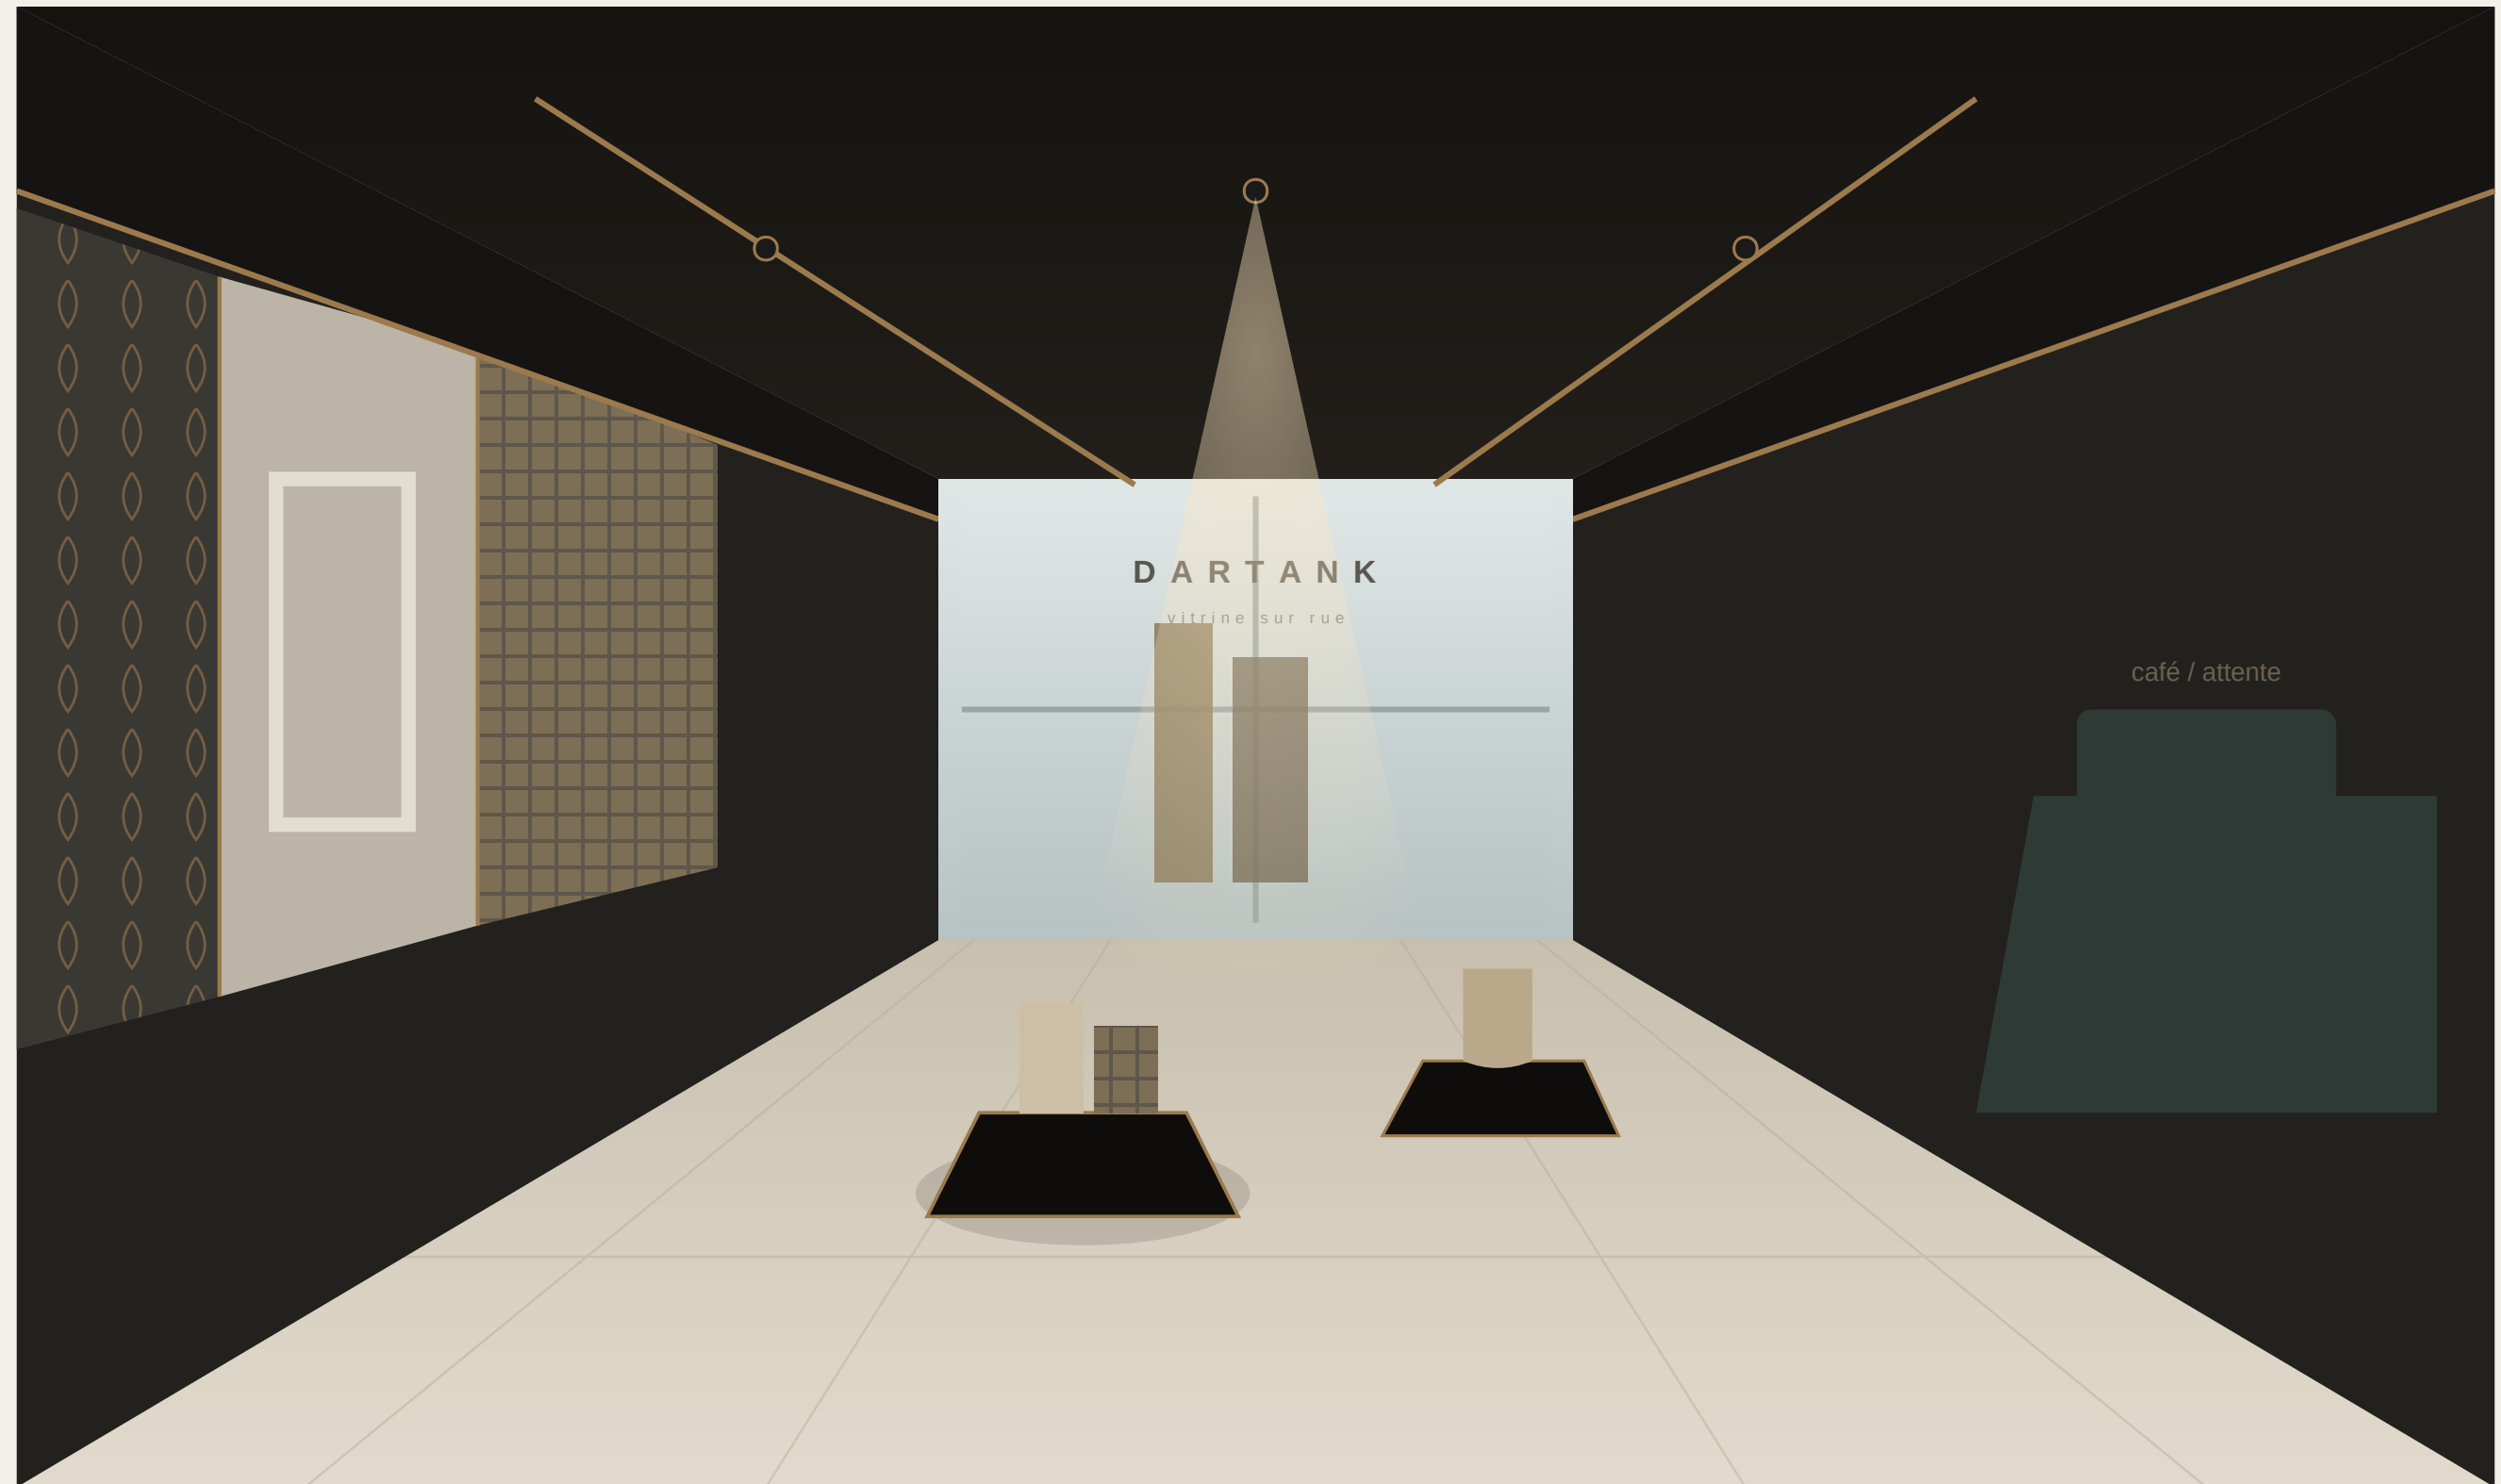

DARTANK · Maison Drapée — Magasin 200 m<sup>2</sup> — Perspective 2 — itération 2 (détail)

**Fond / rue** — Vitrine baignée de lumière naturelle, produit phare en contre-jour

**Gauche** — Room sets (papier peint, moulures, mosaïque)

**Droite** — Coin café / attente en velours vert

**Centre** — Podiums produits guidant le regard vers la vitrine



| POSTE                                                             | BAS (€ HT) | HAUT (€ HT) | RÉPARTITION |
|-------------------------------------------------------------------|------------|-------------|-------------|
| Gros œuvre · cloisons · sols · plafonds                           | 28 000     | 42 000      | <div></div> |
| Agencement menuiserie (comptoir, accueil, matériauthèque)         | 35 000     | 55 000      | <div></div> |
| Podiums modulaires (6) + kits par univers                         | 18 000     | 28 000      | <div></div> |
| Room sets (3) — structures + décors                               | 12 000     | 20 000      | <div></div> |
| Éclairage scénographique (rails, spots, LED, pilotage DALI)       | 22 000     | 34 000      | <div></div> |
| Vitrine · enseigne · signalétique (logo, lettres laiton, plaques) | 16 000     | 26 000      | <div></div> |
| Mobilier (table prescription, café/lounge, sièges)                | 9 000      | 15 000      | <div></div> |
| Digital (écran catalogue, écran projet, écran vitrine)            | 6 000      | 11 000      | <div></div> |
| Électricité · CVC · réseaux · sécurité                            | 14 000     | 22 000      | <div></div> |
| Études · honoraires · divers & aléas (~10%)                       | 18 000     | 28 000      | <div></div> |

TOTAL ESTIMÉ

178 000

281 000

soit ≈ 890 – 1 405 € HT / m²

PHASAGE POSSIBLE

LOT 1 — Coque & image (ouverture)

Gros œuvre, sols, éclairage de base, façade/enseigne, accueil, comptoir

LOT 2 — Merchandising

Podiums + kits, matériauthèque, écrans catalogue, mise en lumière scéno

LOT 3 — Expérience & pro

Room sets complets, prescription, café/lounge, signalétique fine

- ☐ Le concept modulaire permet d'ouvrir avec le LOT 1 puis d'enrichir podiums & room sets progressivement (CAPEX étalé).

Renouvellement annuel (kits/décors) ≈ 5–8 000 € HT.

HYPOTHÈSES & RÉSERVES

- ☐ Ordre de grandeur, hors foncier & loyer.
- ☐ Local supposé livré « brut amélioré ».
- ☐ Prix France, gamme premium, 2026.
- ☐ Hors stock marchandise & échantillons.
- ☐ Hors TVA, assurances, frais financiers.
- ☐ À affiner par consultation d'entreprises.

Leviers d'économie :

socle podium standardisé · rails évolutifs ·  
décors room sets en rotation · digital ciblé.

Estimation indicative destinée à cadrer le projet — ne vaut pas devis.