



DARTANK

D É C O R A T I O N A R C H I T E C T U R A L E

MAGASIN-SHOWROOM PREMIUM

DOSSIER D'AMÉNAGEMENT — 200 m²

PLAN · FAÇADE · PODIUMS · ROOM SETS · ÉCLAIRAGE · MATÉRIAUX · SIGNALÉTIQUE

en collaboration avec MAISON DRAPÉE — papiers peints

CONCEPT & PLANCHES

01	Plan d'aménagement 2D + parcours	p. 3
02	Façade + vitrine	p. 4
03	Showroom produits — podiums	p. 5
04	Murs (room sets) + matériauthèque	p. 6
05	Vue perspective 1	p. 7
06	Concept d'éclairage scénographique	p. 8
07	Mood board matériaux & finitions	p. 9
08	Signalétique, vitrine & logo	p. 10

DÉTAILS TECHNIQUES

09	Plan coté — dimensions	p. 11
10	Détail podium modulaire	p. 12
11	Nomenclature des finitions	p. 13
12	Vue perspective 2 (vitrine, jour)	p. 14
13	Budget indicatif par poste	p. 15

EN BREF

- 200 m² · 9 zones · parcours guidé
- Sélection curatée + matériauthèque + catalogue
- Podiums & room sets modulaires, renouvelables
- Éclairage scénographique, 4 scénarios
- Anthracite #1A1A1A + bronze #9C7A4D


Budget indicatif ≈ 178–281 k€ HT

DARTANK

MAGASIN-SHOWROOM — PLAN D'AMÉNAGEMENT 2D

SÉLECTION CURATÉE · PARCOURS GUIDÉ

≈ 200 m² (12 × 17 m) · éch. ≈ 1:65 · cotes en m

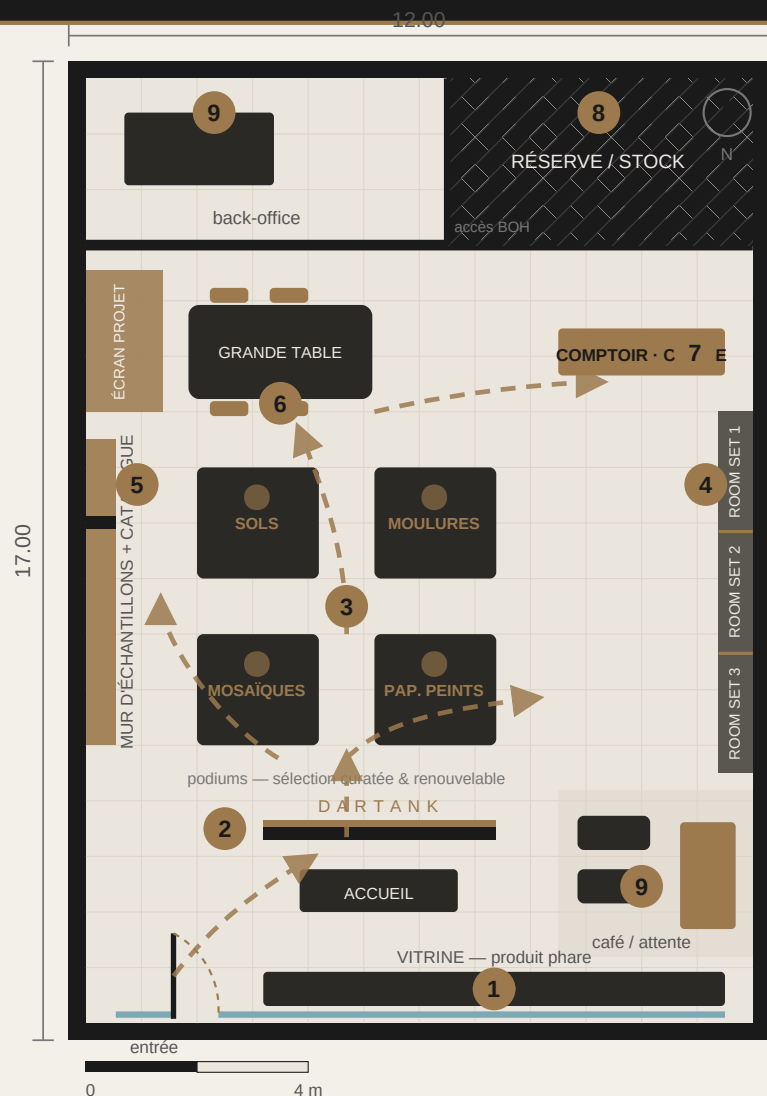


PROGRAMME

- 1 **Façade · enseigne · vitrine**
Produit phare mis en scène
 - 2 **Accueil + mur signature**
Logo · matière · lumière
 - 3 **Showroom produits (podiums)**
Univers curatés & renouvelables
 - 4 **Ambiances scénarisées x3**
Room sets en situation réelle
 - 5 **Matériauthèque + catalogue digital**
Accès au reste de la gamme
 - 6 **Prescription / consultation**
Grande table · écran · nuanciers
 - 7 **Comptoir de vente + caisse**
 - 8 **Réserve / stock**
Gammes à rotation rapide
 - 9 **Back-office + café / attente**
Recevoir & patienter confortablement
- > Parcours client guidé

□ Le magasin expose une sélection curatée ; le reste de la gamme est accessible via la matériauthèque + le catalogue digital (commande sur projet).

PALETTE

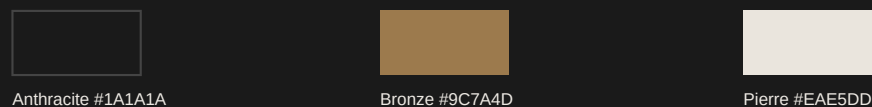

SURFACES INDICATIVES

Showroom produits + podiums	≈ 55 m ²	Café / attente	≈ 14 m ²
Ambiances scénarisées (room sets)	≈ 28 m ²	Matériauthèque + catalogue	≈ 12 m ²
Accueil + signature + vitrine	≈ 24 m ²	Back-office	≈ 12 m ²
Prescription / consultation	≈ 18 m ²	Comptoir + caisse	≈ 11 m ²
Réserve / stock	≈ 18 m ²	Circulation	≈ 8 m ²

TOTAL

≈ 200 m²

Présentoirs modulables · podiums renouvelables · rails d'éclairage évolutifs

DARTANK · Maison Drapée — Magasin-showroom 200 m² — Vue d'ensemble (itération 0)

DARTANK


FAÇADE + VITRINE — ÉLÉVATION

ENSEIGNE & MISE EN SCÈNE PRODUIT PHARE

L 12.00 × H 4.00 m · éch. ≈ 1:60




VUE DE NUIT — ENSEIGNE & VITRINE RÉTROÉCLAIRÉES

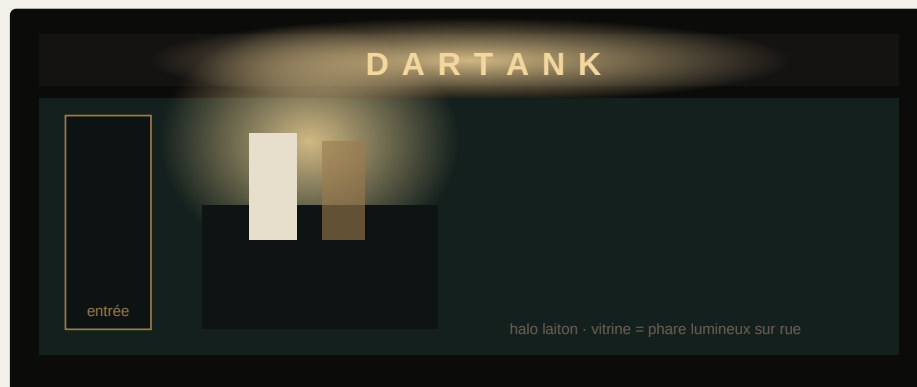

PRINCIPE & MATIÈRES

- Enseigne : lettres boîtier laiton brossé + emblème, halo LED 3000K
- Vitrine plein cintre : un seul produit phare scénarisé, podium noir mis en lumière — renouvelé à chaque collection / saison
- Châssis anthracite mat, montants fins, verre extra-clair
- Pylône latéral anthracite avec logotype vertical (repère de loin)
- Entrée vitrée à gauche, poignée bâton laiton


Objectif : lisibilité premium jour & nuit, vitrine = aimant sur rue.

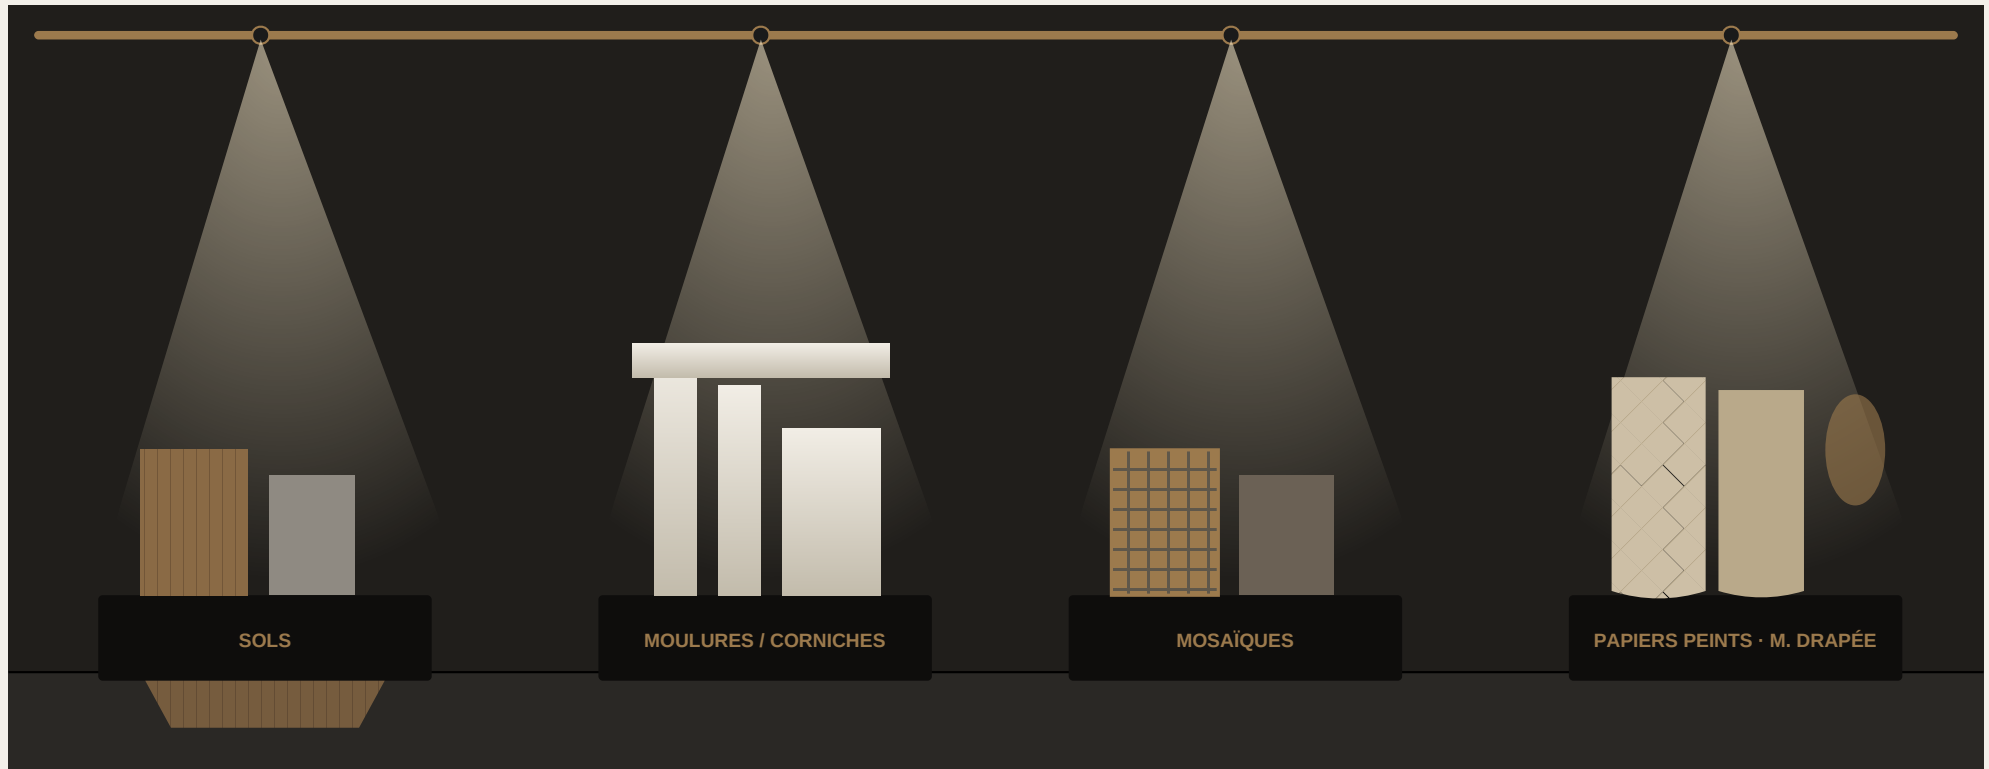

SYSTÈME DE PRÉSENTATION

- Podiums noirs mats sur fond anthracite — produit isolé, mis en lumière
 - 1 podium = 1 univers ; rotation/renouvellement à chaque collection
 - Présentoirs modulables : stands inclinés (sols), bras (moulures), cadres (mosaïques), barres + lest (papiers peints)
 - Échantillon "à toucher" + plaquette bronze (réf. + QR catalogue)
- Curaté, pas exhaustif — le reste via la matériauthèque (zone 5).**


IMPLANTATION (rappel plan)

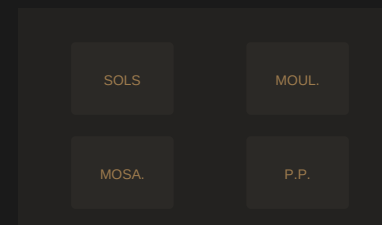


4 podiums au cœur du magasin, circulation périphérique fluide, vues plongeantes depuis l'entrée.

Espacement ≥ 1.2 m entre podiums (confort & accessibilité PMR).

MUR EST — 3 AMBIANCES SCÉNARISÉES (ROOM SETS)

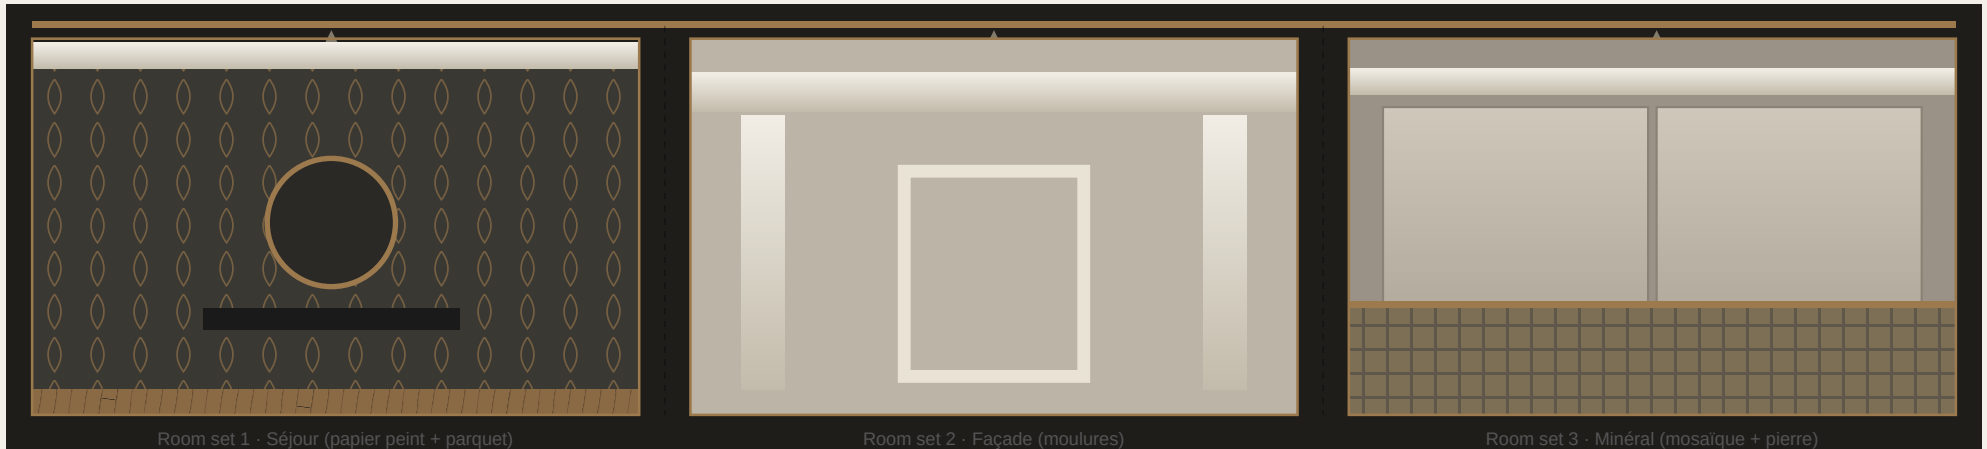

MUR OUEST — MATÉRIAUTHÈQUE (RESTE DE LA GAMME) + ÉCRAN CATALOGUE DIGITAL

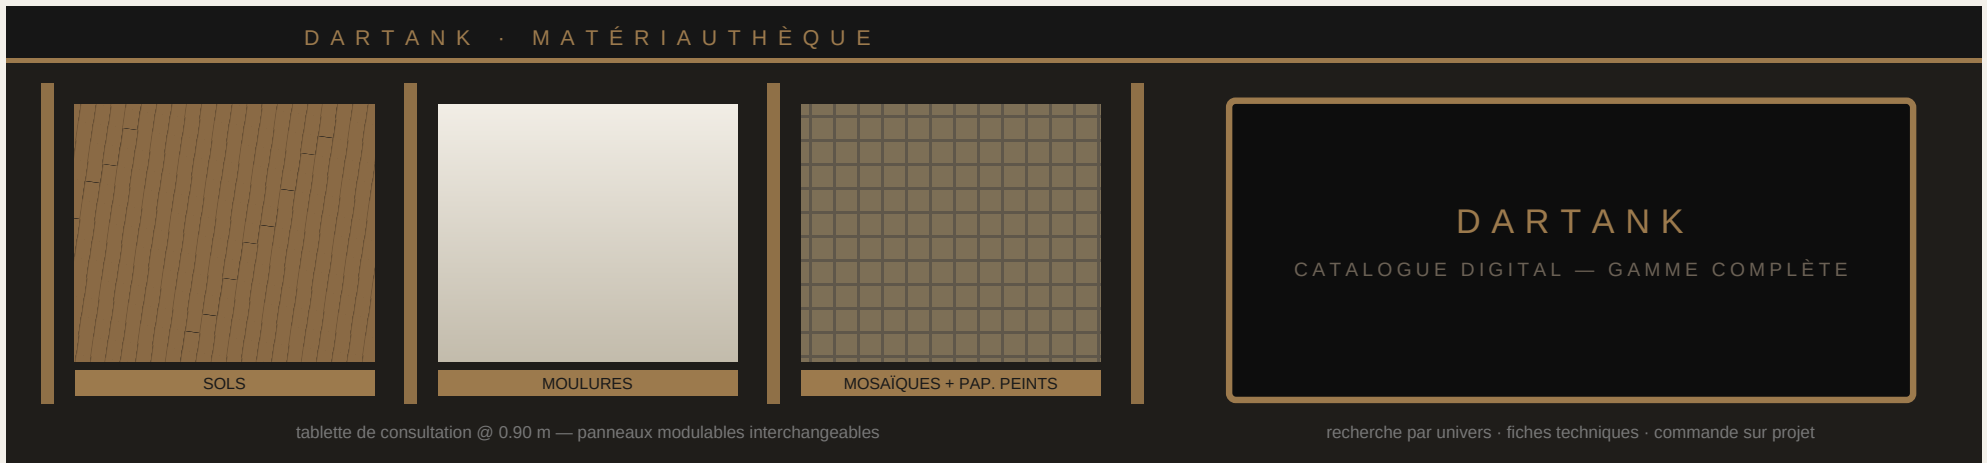

Le mur d'échantillons + l'écran donnent accès à TOUTE la gamme non exposée — sans surcharger le magasin.

DARTANK

MAGASIN — VUE PERSPECTIVE

DEPUIS L'ENTRÉE VERS LE MUR SIGNATURE

podiums & room sets sous éclairage scénographique




DARTANK · Maison Drapée — Magasin 200 m² — Perspective — iteration 1

Centre — Podiums produits par univers, isolés & mis en lumière

Gauche — Matériauthèque (reste de la gamme) + tablette de consultation

Droite — Room sets : papier peint Maison Drapée, moulures de façade

Fond — Mur signature rétroéclairé + accueil ; rails de spots scénographiques

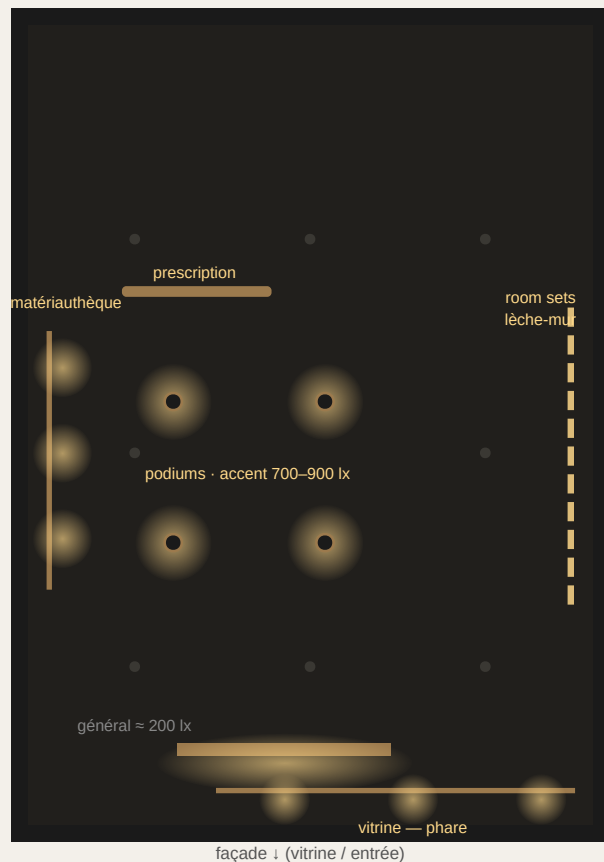

APPAREILS & PARAMÈTRES

- Spot accent sur rail — podiums & vitrine, faisceau serré 15–24°
- Lèche-mur (wall-grazing) — room sets & matériauthèque
- Downlight général encastré — circulation & confort
- Suspension linéaire — table de prescription & accueil

Température	2700–3000 K	Accent podiums	700–900 lx
Rendu couleurs (matière)	IRC > 90	Room sets	500–700 lx
Général / circulation	200 lx	Vitrine (phare)	1000 lx

Rails alimentés sur tout le plafond : ajout/déplacement de spots sans travaux —
l'éclairage suit le renouvellement des podiums & des room sets.

SCÉNARIOS (gradation DALI)

1 · JOUR COMMERÇANT

Général 100% · accents podiums 80% · vitrine 100% — accueillant & lisible

2 · PRESCRIPTION (pros)

Table 500 lx · accents 100% · matériauthèque renforcée — comparaison fidèle

3 · SOIRÉE / ÉVÈNEMENT

Général 30% · accents + lèche-mur 100% · signature & vitrine — atmosphère

4 · VITRINE NUIT

Enseigne + vitrine produit phare + 1 room set allumés — présence sur rue 24/7


- Pilotage centralisé, scénarios mémorisés, horloge astronomique pour la vitrine.
Mise en lumière = outil de merchandising : on dirige le regard vers le produit phare.

DARTANK

MATÉRIAUX & FINITIONS — MOOD BOARD

PALETTE PREMIUM · LIGNES ÉPURÉES

matériaux nobles · accent bronze/laiton

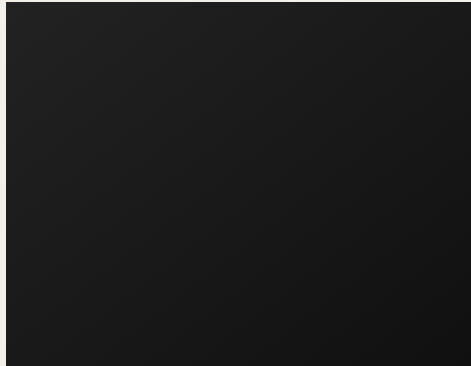

Anthracite profond #1A1A1A

Microciment / peinture mate — murs, mobilier, signature




Bronze / laiton brossé #9C7A4D

Détails, lettrage, mains courantes, piétements, rails




Pierre claire #EAE5DD

Sol showroom, tablettes — respiration claire

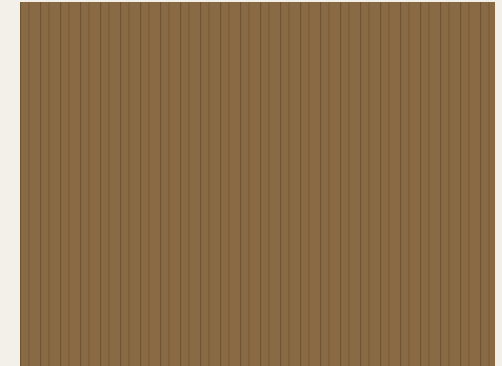

Chêne fumé sol / mobilier

Assises, plateau de table, plinthes — chaleur

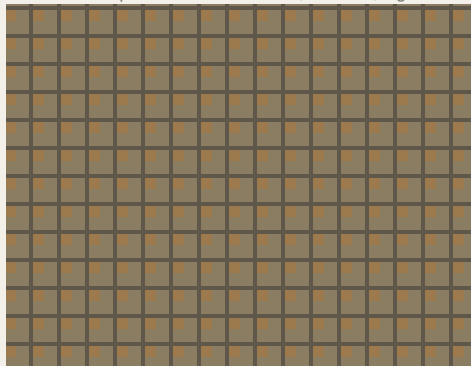

Mosaïque pierre & or accent

Touches ponctuelles, soubassements d'ambiance



Papier peint Maison Drapée

Ambiance séjour — lés tendus, textile mural



Velours vert profond #2E3A35


Assise d'appoint / rappel coloré chic



Verre & miroir fumé

Cloisons, vitrine, jeux de reflets & profondeur

PALETTE

 

Anthracite
#1A1A1A




Bronze
#9C7A4D



Pierre
#EAE5DD



Taupe
#5A5650

 

Vert prof.
#2E3A35



Chêne
#8A6A45

PRINCIPES D'ASSOCIATION

- 80% neutres (anthracite + pierre), 15% bois, 5% bronze en touches — la matière exposée prime.
- Mat contre brillant : fonds mats, accents métalliques brossés & reflets de verre.
- Finitions tactiles — un showroom où l'on touche.

DARTANK · Maison Drapée — Magasin 200 m² — Mood board matériaux & finitions — itération 1

DARTANK

SIGNALÉTIQUE, VITRINE & LOGO — IDENTITÉ DE MARQUE

ENSEIGNE · VITRINE · MUR SIGNATURE

emblème portail · logotype · endossement

LOGO PRINCIPAL



DARTANK

DÉCORATION ARCHITECTURALE

ENSEIGNE DE FAÇADE — LETTRES BOÎTIER LAITON, RÉTROÉCLAIRAGE HALO



DARTANK

entrée

MUR D'ACCUEIL — LETTRES BRONZE BROSSÉ + HALO



DARTANK

DÉCORATION ARCHITECTURALE

— en collaboration avec —
Maison Drapée

VERSION CLAIRE & ENDOSSEMENT



DARTANK

DÉCORATION ARCHITECTURALE

marque sœur · papiers peints
Maison Drapée

PLAQUES DE ZONE — BRONZE SUR ANTHRACITE

01 · SOLS

02 · MOULURES

03 · MOSAÏQUES

04 · PAPIERS P.

PRESCRIPTION / CONSULTATION

Plaquettes gravées laiton, fixation aimantée — repositionnables.
Pictogrammes minimalistes, même langage que l'étiquetage produit.
Numérotation = renvoi au plan & au catalogue digital.

TYPOGRAPHIE & CONSTRUCTION

- Logotype : capitales, linéale élégante, interlettrage large (≈ +10%)
 - Emblème "portail" = évocation moulure / façade architecturale
 - Endossement Maison Drapée en italique fin, jamais plus grand que DARTANK
- Zone de protection = hauteur du « D » sur tout le pourtour.

MATIÈRES & FABRICATION

- Enseigne : lettres boîtier laiton brossé, rétroéclairage halo LED 3000K
 - Mur signature : lettres relief bronze brossé sur fond microciment anthracite
 - Vitrine : logo & mention dépolis / sérigraphiés sur verre, lettrage laiton
- Cohérence façade ↔ vitrine ↔ intérieur ↔ étiquette produit ↔ catalogue digital.

DARTANK · Maison Drapée — Magasin 200 m² — Signalétique, vitrine & logo — itération 1

DARTANK

PLAN COTÉ — DIMENSIONS INDICATIVES

12.00 × 17.00 m = 204 m²

éch. ≈ 1:65 · cotes en m



CLEARANCES & ACCESSIBILITÉ

Allées principales	≥ 1.50 m
Entre podiums	≥ 1.20 m
Porte d'entrée (libre)	1.40 m
Accès réserve / BOH	0.90 m
Hauteur sous plafond	3.20 m
Aire de rotation PMR	Ø 1.50 m

- Toutes cotes indicatives, à relever sur site avant exécution.
- Trame structurelle à confirmer (poteaux, réseaux, issues de secours).
- Conformité ERP / accessibilité PMR à valider avec bureau de contrôle.

Surface utile ≈ 204 m² (hors cloisons).

RÉPARTITION PAR BANDE (profondeur)

Bande fond (BOH)	3.00 m	réserve + back-office
Bande service	3.30 m	prescription + comptoir/caisse
Bande showroom	6.20 m	podiums + room sets + matériauthèque
Bande accueil	3.30 m	accueil + signature + café
Bande façade	1.20 m	vitrine + entrée
Profondeur totale	17.00 m	


DARTANK

PODIUM MODULAIRE — DÉTAIL DE PRINCIPE

PRÉSENTOIR ÉVOLUTIF & RENOUVELABLE

cotes en m · détail ≈ 1:20

A · ÉLÉVATION TYPE

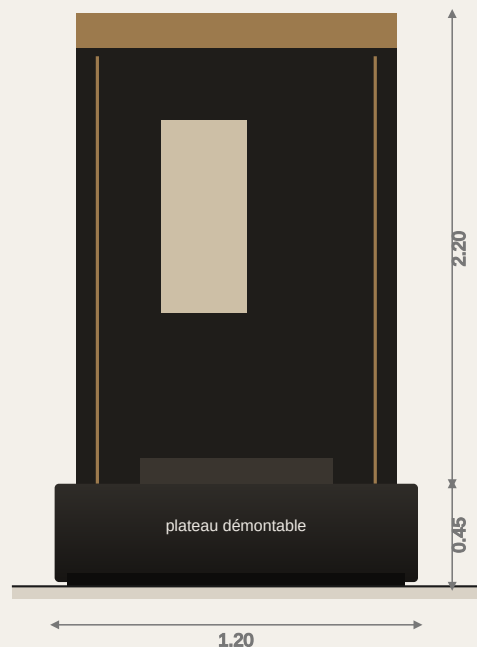

B · COUPE — CONSTRUCTION



SPÉCIFICATIONS

Empreinte socle	1.20 × 0.80 m
Hauteur plateau	0.45 m
Panneau dossier	H 2.20 m
Caisson	MDF laqué mat
Plateau	amovible / interchangeable
Socle	en retrait (effet flottant)
Accroche dossier	rail crémaillère bronze
Éclairage	spot rail + LED option

MODULARITÉ


- 1 socle commun → 4 kits de présentation
- Changement d'univers = changement de plateau + dossier, sans toucher au socle
- Renouvellement par collection / saison
- Déplaçable (patins) pour réagencer le magasin
- Plaquette bronze réf. + QR → catalogue

ÉCONOMIE

Investissement concentré sur un socle durable ; les kits (peu coûteux) tournent. Vitrine toujours « neuve » à budget maîtrisé.

Cible : 4 podiums + 2 podiums d'appoint pour temps forts / nouveautés.

C · VARIANTES DE PRÉSENTOIR (même socle)

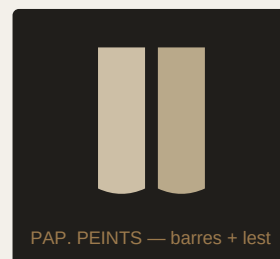

ZONE	SOL	MURS / FONDS	ÉCLAIRAGE	MOBILIER / AGENCEMENT
1 · Façade / vitrine	grand format pierre clr	châssis anthracite, verre extra-clair	spots accent 1000 lx + halo enseigne	podium phare noir laqué
2 · Accueil + signature	pierre claire mate	microciment anthracite + logo bronze	wash mural + suspension accueil	banque d'accueil laiton/anthracite
3 · Showroom podiums	pierre claire / microciment	anthracite mat (fond podiums)	spots serrés 700–900 lx / podium	podiums modulaires MDF laqué
4 · Room sets (x3)	parquet / mosaïque selon set	papier peint, moulures, pierre montés	lèche-mur 500–700 lx	décors interchangeables, cadres bronze
5 · Matériauthèque	pierre claire	panneaux modulables / crémaillère bronze	lèche-mur + spots + écran rétroécl.	tablette 0.90 m, écran catalogue
6 · Prescription	parquet chêne fumé	anthracite + velours vert (acoustique)	suspension linéaire 500 lx, 3000K	grande table, écran projet, nuanciers
7 · Comptoir + caisse	pierre claire	parement anthracite + logo bronze	suspension + accent caisse	comptoir laiton brossé, back-counter
8 · Réserve / stock	résine / béton ciré	peinture lessivable claire	réglettes LED fonctionnelles 300 lx	rayonnages métal, casiers gammes rapides
9 · Back-office + café	chêne fumé / pierre	anthracite + touche velours vert	général doux 200 lx + liseuses	bureau, lounge, point café laiton

RÉFÉRENCES DE FINITION

-  Microciment anthracite mat — murs signature, fonds podiums
-  Laiton / bronze brossé — logo, comptoir, rails, détails
-  Pierre claire grand format — sol showroom, circulation
-  Chêne fumé — parquet prescription, mobilier, plinthes
-  Velours vert profond — assises, panneaux acoustiques

Toutes finitions à valider sur échantillons physiques (mock-up recommandé).

PRINCIPES TRANSVERSES

- ☐ Fonds mats & sombres = la matière exposée
prime (zéro reflet parasite)
- ☐ Bronze = fil rouge de marque (5% des surfaces)
- ☐ Sol clair continu = respiration & lisibilité
- ☐ Éclairage 2700–3000K, IRC>90 partout
- ☐ Acoustique traitée en prescription & café
- ☐ Tout l'agencement = modulaire & déplaçable


Cohérence avec le showroom 70 m² (même ADN).

DARTANK

MAGASIN — VUE PERSPECTIVE 2 (VERS LA VITRINE)

AMBIANCE JOUR · LUMIÈRE NATURELLE

depuis le fond du magasin vers la rue

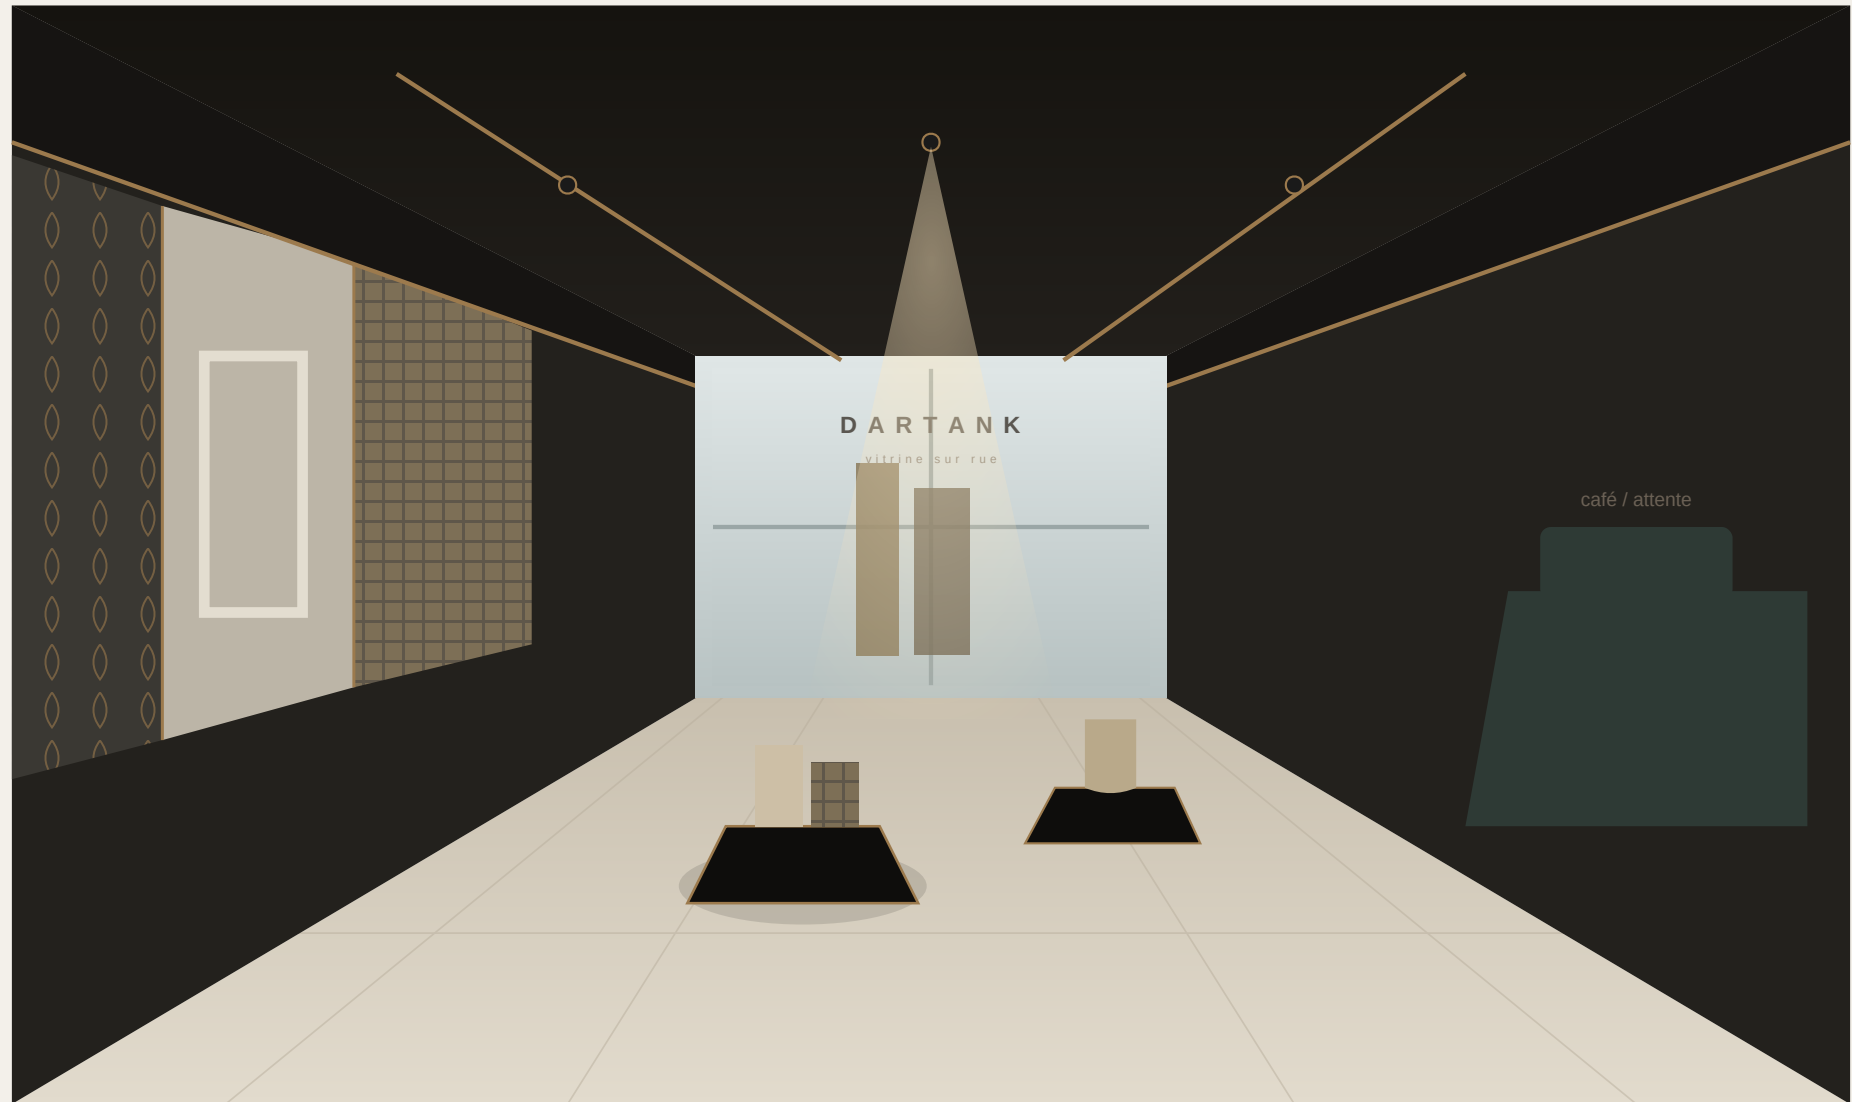

DARTANK · Maison Drapée — Magasin 200 m² — Perspective 2 — itération 2 (détail)

Fond / rue — Vitrine baignée de lumière naturelle, produit phare en contre-jour

Gauche — Room sets (papier peint, moulures, mosaïque)

Droite — Coin café / attente en velours vert

Centre — Podiums produits guidant le regard vers la vitrine

POSTE	BAS (€ HT)	HAUT (€ HT)	RÉPARTITION
Gros œuvre · cloisons · sols · plafonds	28 000	42 000	
Agencement menuiserie (comptoir, accueil, matériauthèque)	35 000	55 000	
Podiums modulaires (6) + kits par univers	18 000	28 000	
Room sets (3) — structures + décors	12 000	20 000	
Éclairage scénographique (rails, spots, LED, pilotage DALI)	22 000	34 000	
Vitrine · enseigne · signalétique (logo, lettres laiton, plaques)	16 000	26 000	
Mobilier (table prescription, café/lounge, sièges)	9 000	15 000	
Digital (écran catalogue, écran projet, écran vitrine)	6 000	11 000	
Électricité · CVC · réseaux · sécurité	14 000	22 000	
Études · honoraires · divers & aléas (~10%)	18 000	28 000	
TOTAL ESTIMÉ	178 000	281 000	soit ≈ 890 – 1 405 € HT / m²

PHASAGE POSSIBLE

LOT 1 — Coque & image (ouverture)

Gros œuvre, sols, éclairage de base, façade/enseigne, accueil, comptoir

LOT 2 — Merchandising

Podiums + kits, matériauthèque, écrans catalogue, mise en lumière scéno

LOT 3 — Expérience & pro

Room sets complets, prescription, café/lounge, signalétique fine

- ☐ Le concept modulaire permet d'ouvrir avec le LOT 1
puis d'enrichir podiums & room sets progressivement (CAPEX étalé).

Renouvellement annuel (kits/décors) ≈ 5–8 000 € HT.

HYPOTHÈSES & RÉSERVES

- ☐ Ordre de grandeur, hors foncier & loyer.
- ☐ Local supposé livré « brut amélioré ».
- ☐ Prix France, gamme premium, 2026.
- ☐ Hors stock marchandise & échantillons.
- ☐ Hors TVA, assurances, frais financiers.
- ☐ À affiner par consultation d'entreprises.

Leviers d'économie :

socle podium standardisé · rails évolutifs ·
décors room sets en rotation · digital ciblé.

Estimation indicative destinée à cadrer le projet — ne vaut pas devis.

DARTANK · Maison Drapée — Magasin 200 m² — Budget indicatif — itération 2 (détail)