

DARTANK

D É C O R A T I O N A R C H I T E C T U R A L E

SHOWROOM DE PRESCRIPTION

DOSSIER D'AMÉNAGEMENT — 70 m²

CONCEPT & ÉLÉVATIONS · ÉCLAIRAGE · MATÉRIAUX · SIGNALÉTIQUE

en collaboration avec MAISON DRAPÉE — papiers peints


01	Plan d'aménagement 2D Zones légendées · cotes · parcours client · palette · surfaces	p. 3
02	Élévation matériauthèque — mur ouest Système modulable · calepinage par gamme · hauteurs de présentation	p. 4
03	Détail montant à crémaillère & formats Coupes techniques · tableau formats / références · étiquetage	p. 5
04	Élévation mur est — 3 ambiances scénarisées Séjour · façade · minéral — produits posés en situation réelle	p. 6
05	Vue perspective d'ambiance Atmosphère générale depuis l'entrée vers l'espace prescription	p. 7
06	Concept d'éclairage Plan de plafond · appareils · 2700–3000 K · IRC>90 · 4 scénarios	p. 8
07	Mood board matériaux & finitions 8 matières nobles · palette · principes d'association	p. 9
08	Signalétique & logo DARTANK Emblème · enseigne façade · mur signature · endossement Maison Drapée	p. 10

DARTANK

DÉCORATION ARCHITECTURALE — SHOWROOM DE PRESCRIPTION

PLAN D'AMÉNAGEMENT 2D

70 m² (7 × 10 m) · éch. ≈ 1:55 · cotes en m

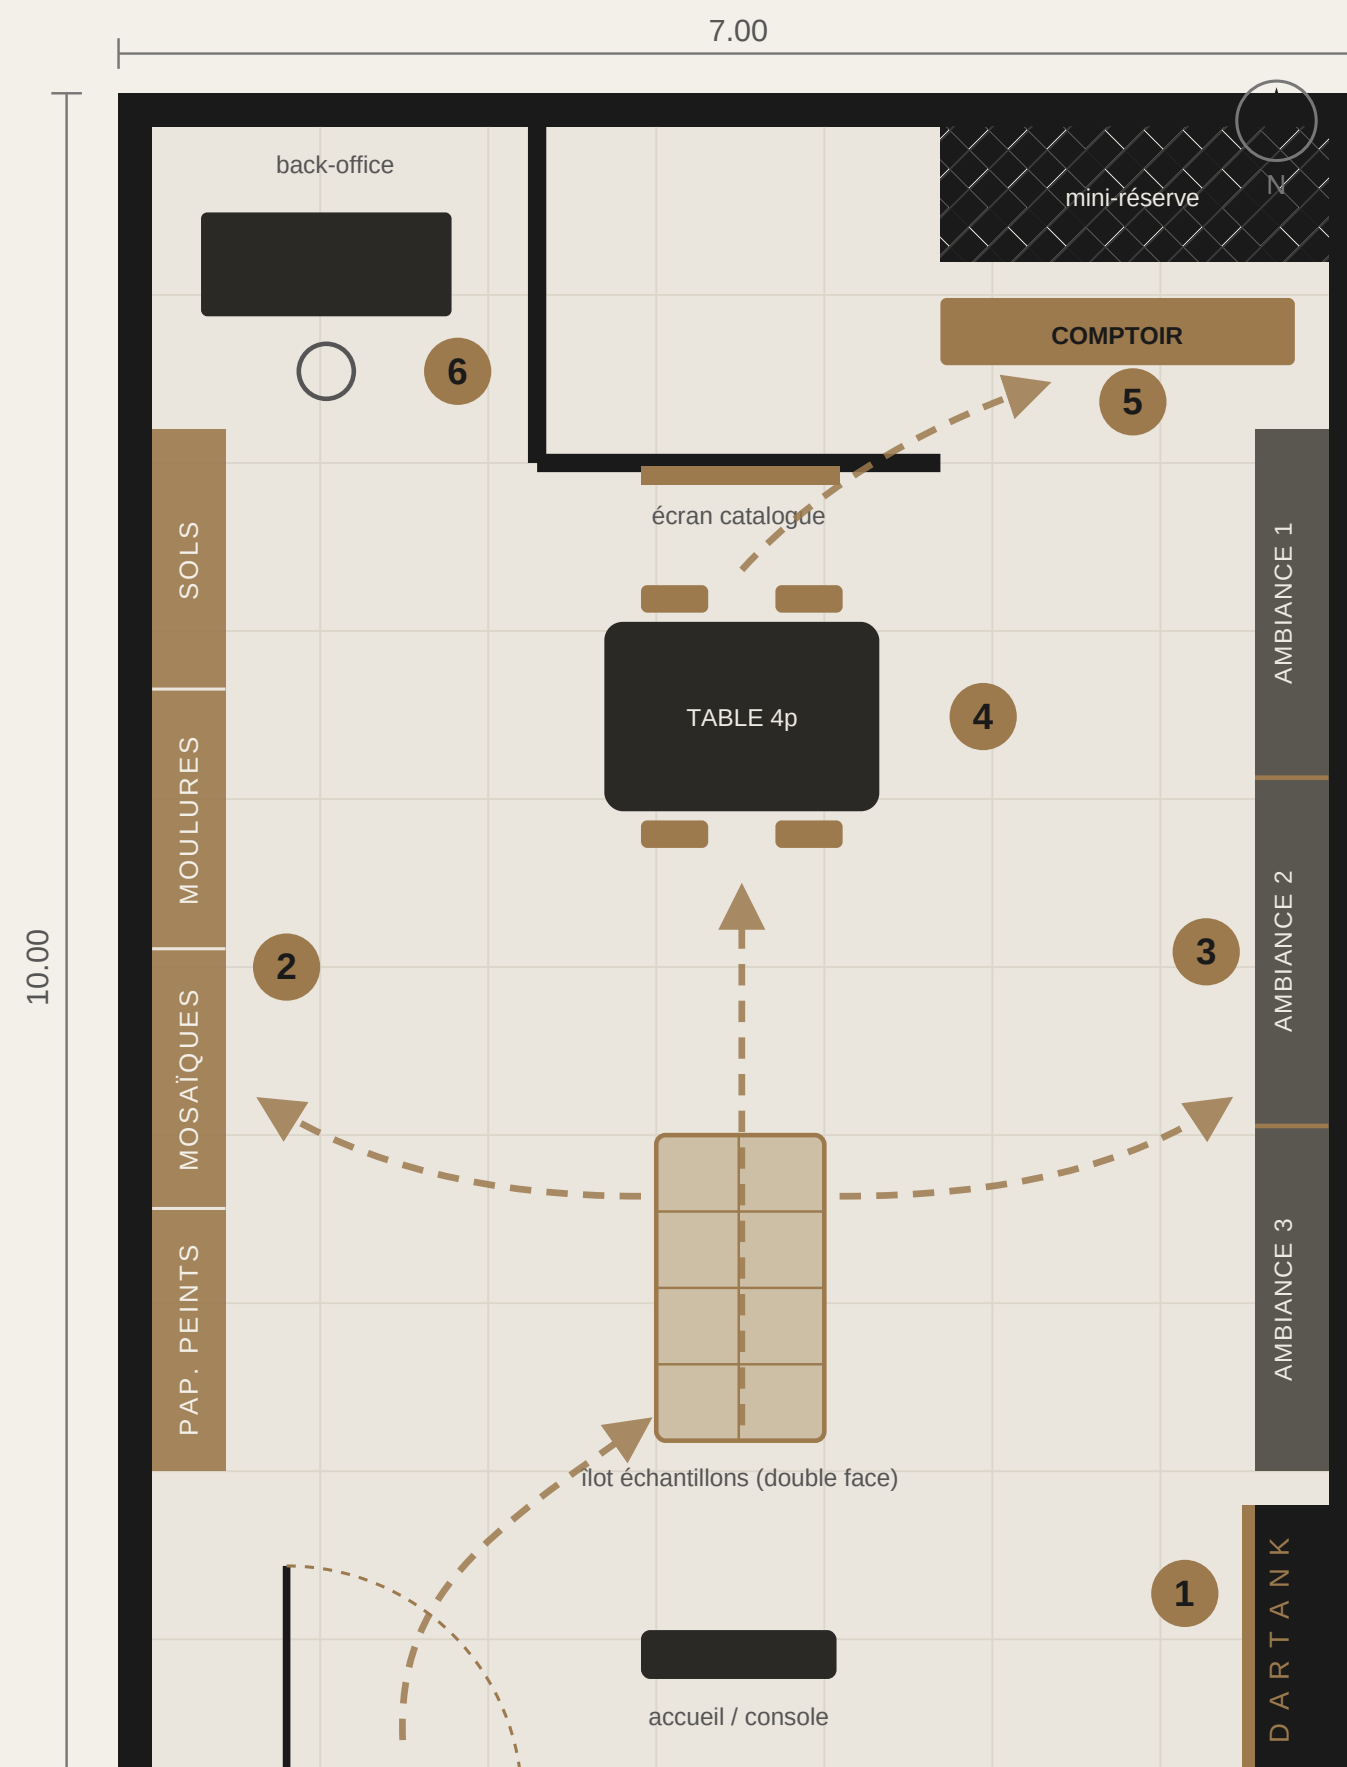

PROGRAMME

- 1 Entrée + mur signature**
Enseigne façade · logo DARTANK
 - 2 Matériauthèque**
Panneaux par gamme (sols, moulures...)
 - 3 Ambiances scénarisées ×3**
Produits posés en situation réelle
 - 4 Prescription / consultation**
Table 4 pers. + écran catalogue
 - 5 Comptoir + mini-réserve**
Gammes à rotation rapide
 - 6 Back-office**
Bureau commerciale
- > Parcours client / circulation

PALETTE

Anthracite #1A1A1A	Bronze #9C7A4D	Pierre #EAE5DD	Taupe #5A5650

SURFACES (indic.)


Matériauthèque + ambiances	≈ 22 m ²
Prescription / consultation	≈ 12 m ²
Entrée / accueil + circulation	≈ 20 m ²
Comptoir + mini-réserve	≈ 9 m ²
Back-office	≈ 5 m ²
TOTAL	≈ 68 m²

DARTANK

MATÉRIAUTHÈQUE — ÉLÉVATION MUR OUEST

SYSTÈME DE PRÉSENTATION MODULABLE

L 6.20 × H 3.20 m · éch. ≈ 1:62 · cotes en m

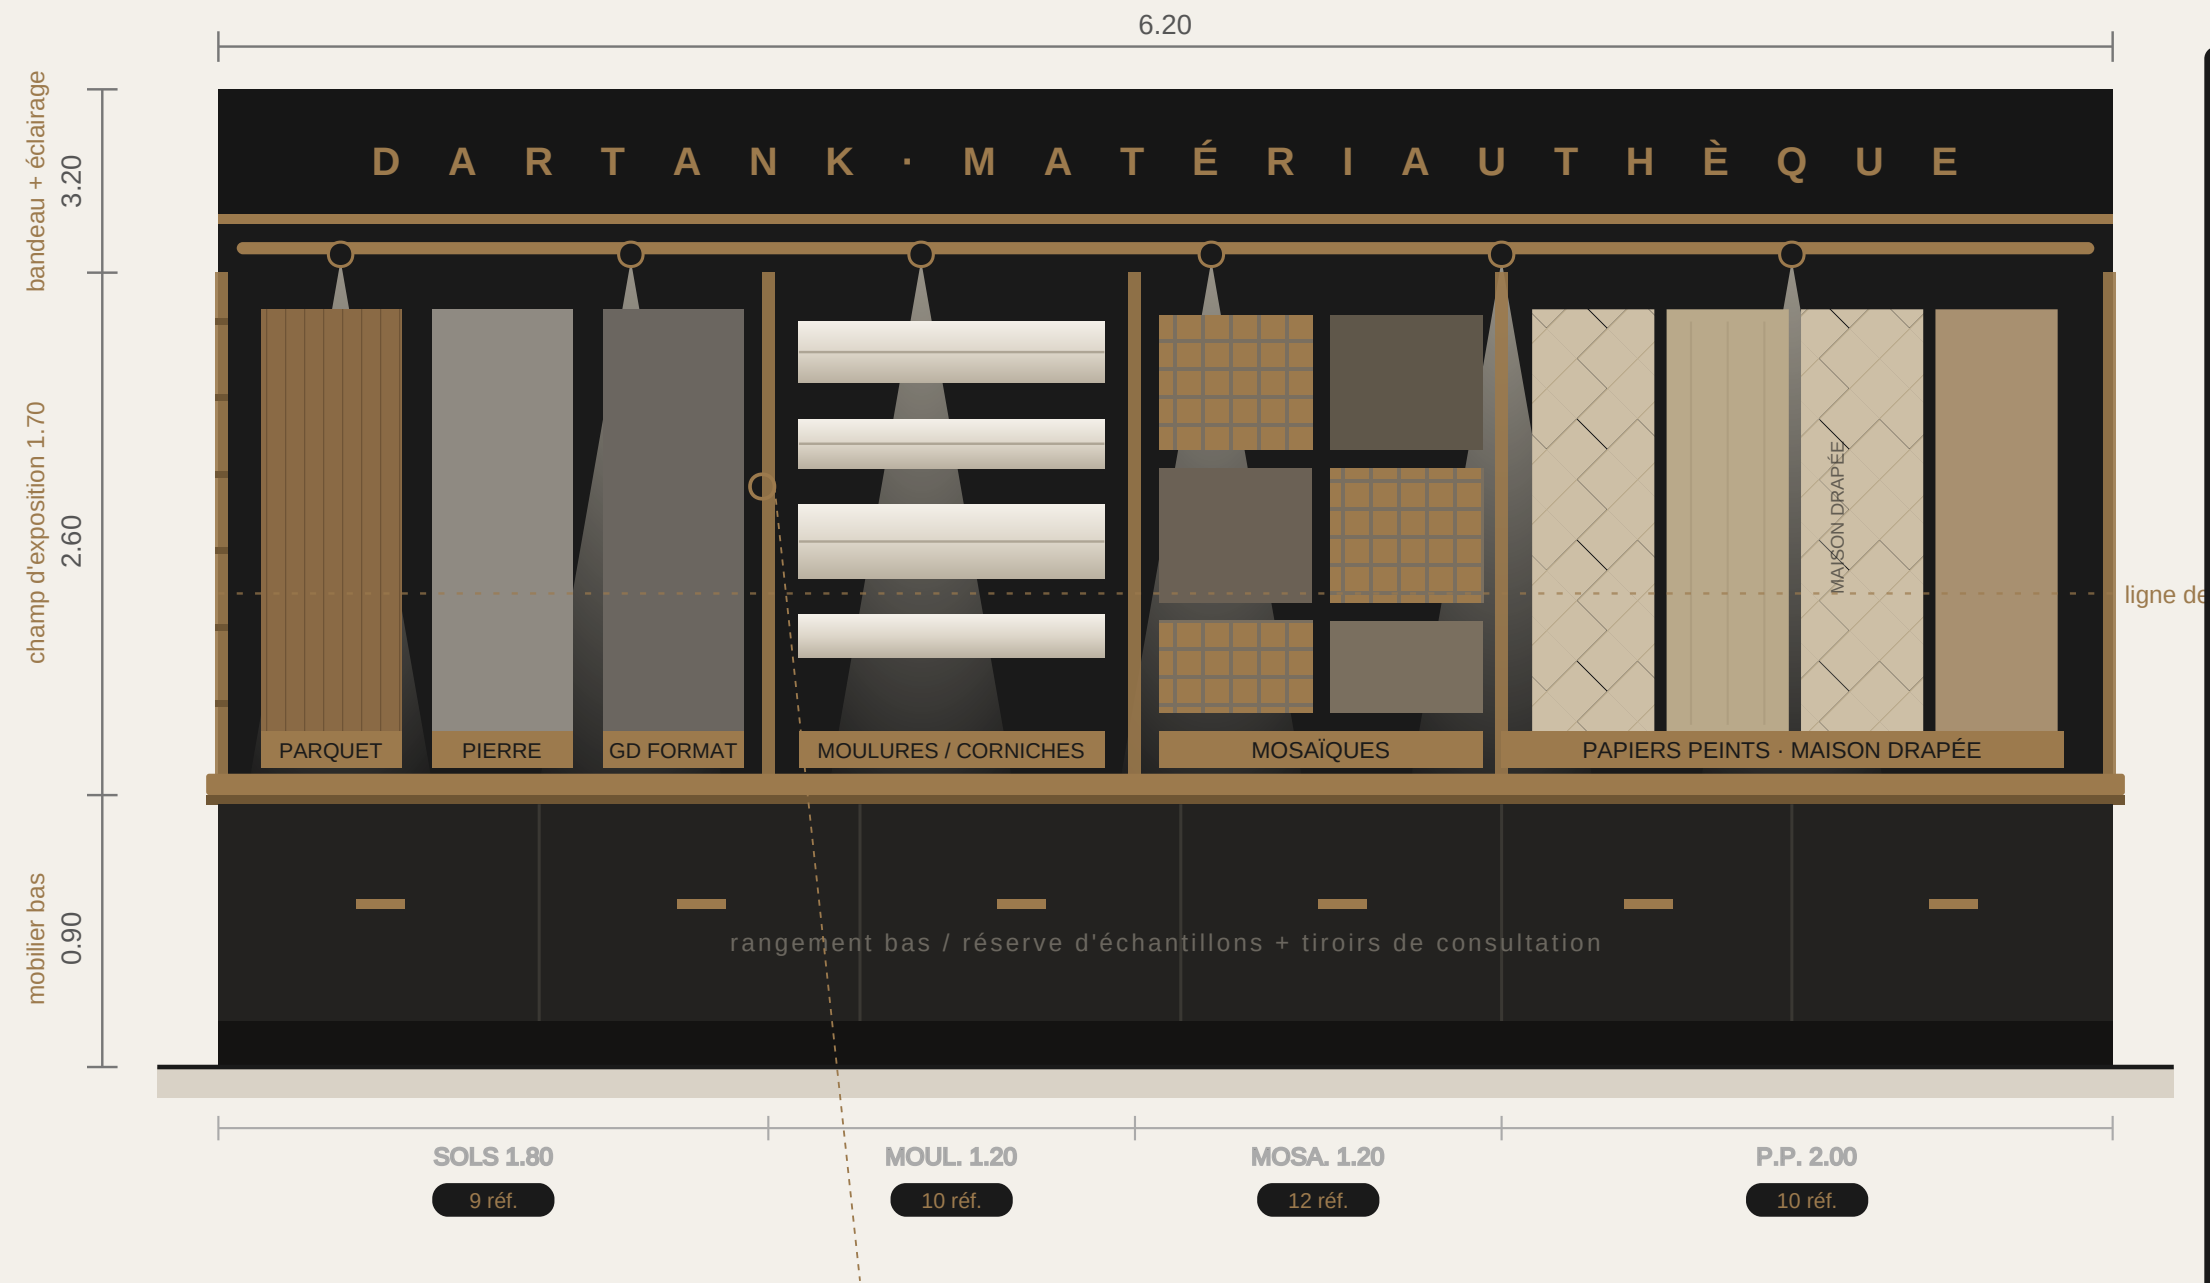

SYSTÈME MODULABLE

- Montants à crémaillère bronze
panneaux clipsables & interchangeables
- Fond anthracite mat
la matière ressort, zéro reflet parasite
- Tablette de consultation @ 0.90 m
pose & comparaison des échantillons
- Réserve intégrée sous tablette
- Rail de spots orientables au plafond

HAUTEURS CLÉS

Échantillon premium (regard)	1.40–1.80
Tablette de travail	0.90
Haut champ d'exposition	2.60
Sous-plafond	3.20

FORMATS PAR GAMME

- Sols — boards 40×60 verticaux
- Moulures — profils réels montés
- Mosaïques — plaques 30×30
- Papiers peints — lés tendus

ÉCONOMIE

Structure fixe (montants + bandeau) ;
seuls les panneaux évoluent au gré des
collections. Réagencement en minutes,
sans travaux.

DARTANK · Maison Drapée — Élévation matériauuthèque (mur ouest) — itération 1


DARTANK

MATÉRIAUTHÈQUE — DÉTAIL MONTANT & FORMATS D'ÉCHANTILLONS


SYSTÈME À CRÉMAILLÈRE

détail ≈ 1:5 · cotes en mm


A · PRINCIPE — ÉCLATÉ

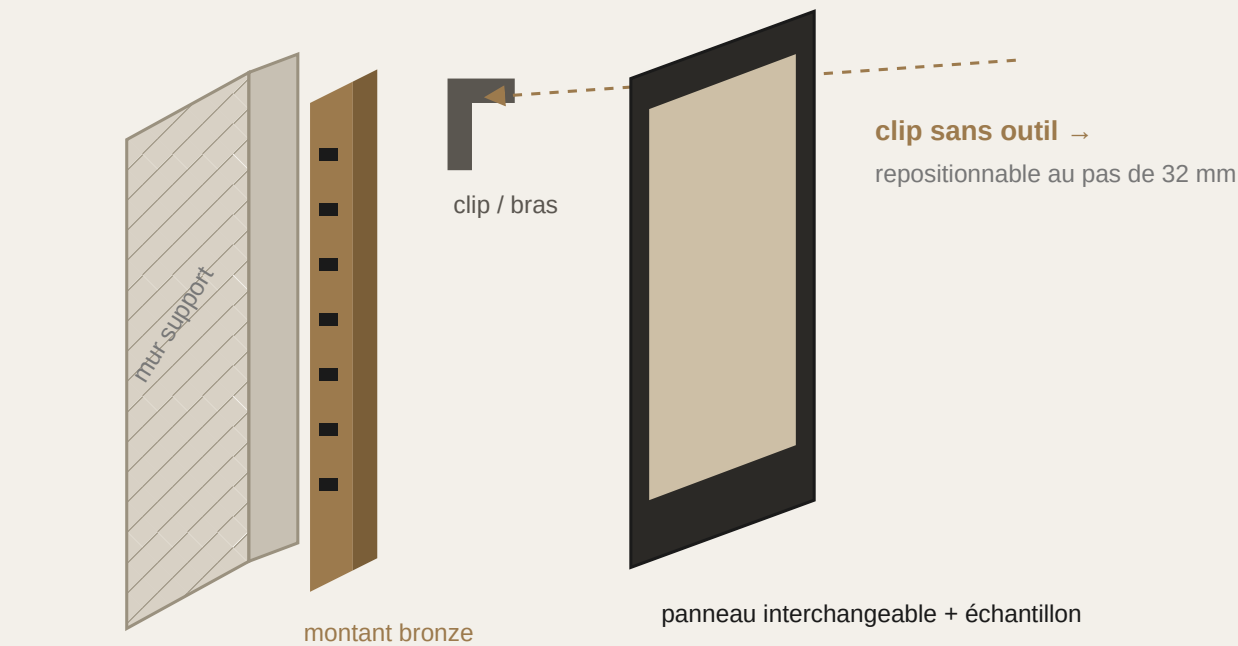

B · COUPE VERTICALE

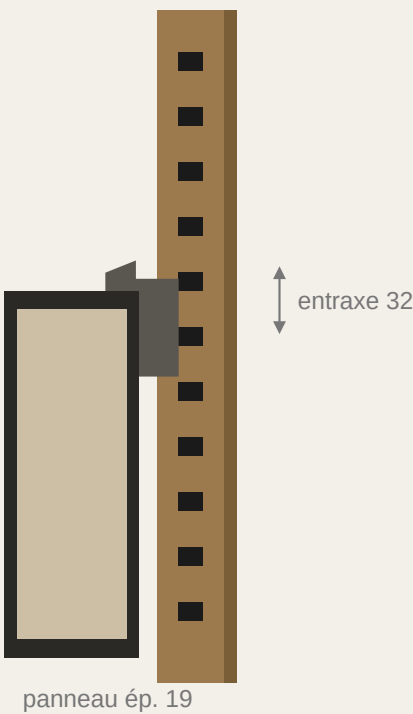

C · COUPE HORIZONTALE

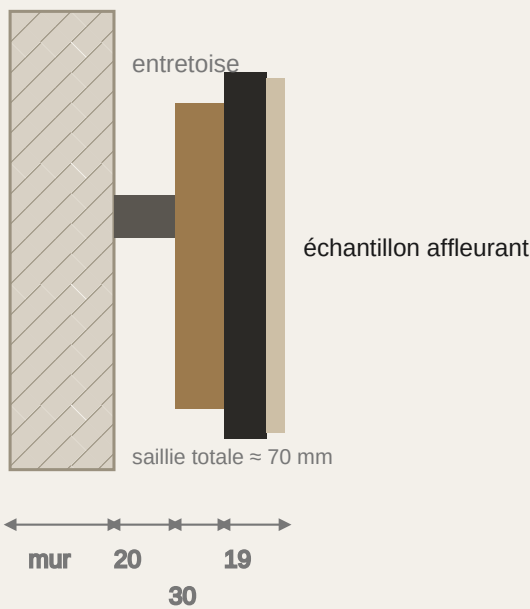

FORMATS & RÉFÉRENCES PAR GAMME

GAMME	FORMAT	SUPPORT	RÉF.
Sols	board 40×60	board clipsé	9
Moulures / corniches	profil réel L.50	bras profilé	10
Mosaïques	plaque 30×30	plaque aimantée	12
Papiers peints + Maison Drapée	lé 50×140	barre + lest bas	10
TOTAL linéaire 6.20 m			41 réf.

ÉTIQUETAGE & RÉFÉRENCEMENT


DARTANK · SOLS

Réf. DK-S-204 · Chêne fumé



- Plaque bronze gravée :
réf. + nom de collection
- QR → fiche technique digitale
(specs, formats dispo, prix prescr.)

PROPORTIONS — RÉÉQUILIBRAGE

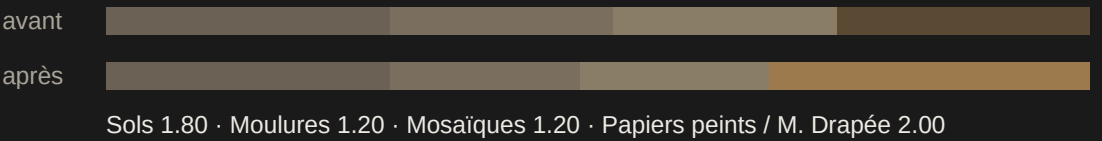


DARTANK · Maison Drapée — Détail montant à crémaillère & formats — itération 1 bis

DARTANK

AMBIANCES SCÉNARISÉES — ÉLÉVATION MUR EST

PRODUITS POSÉS EN SITUATION RÉELLE

L 6.00 × H 3.20 m · éch. ≈ 1:60

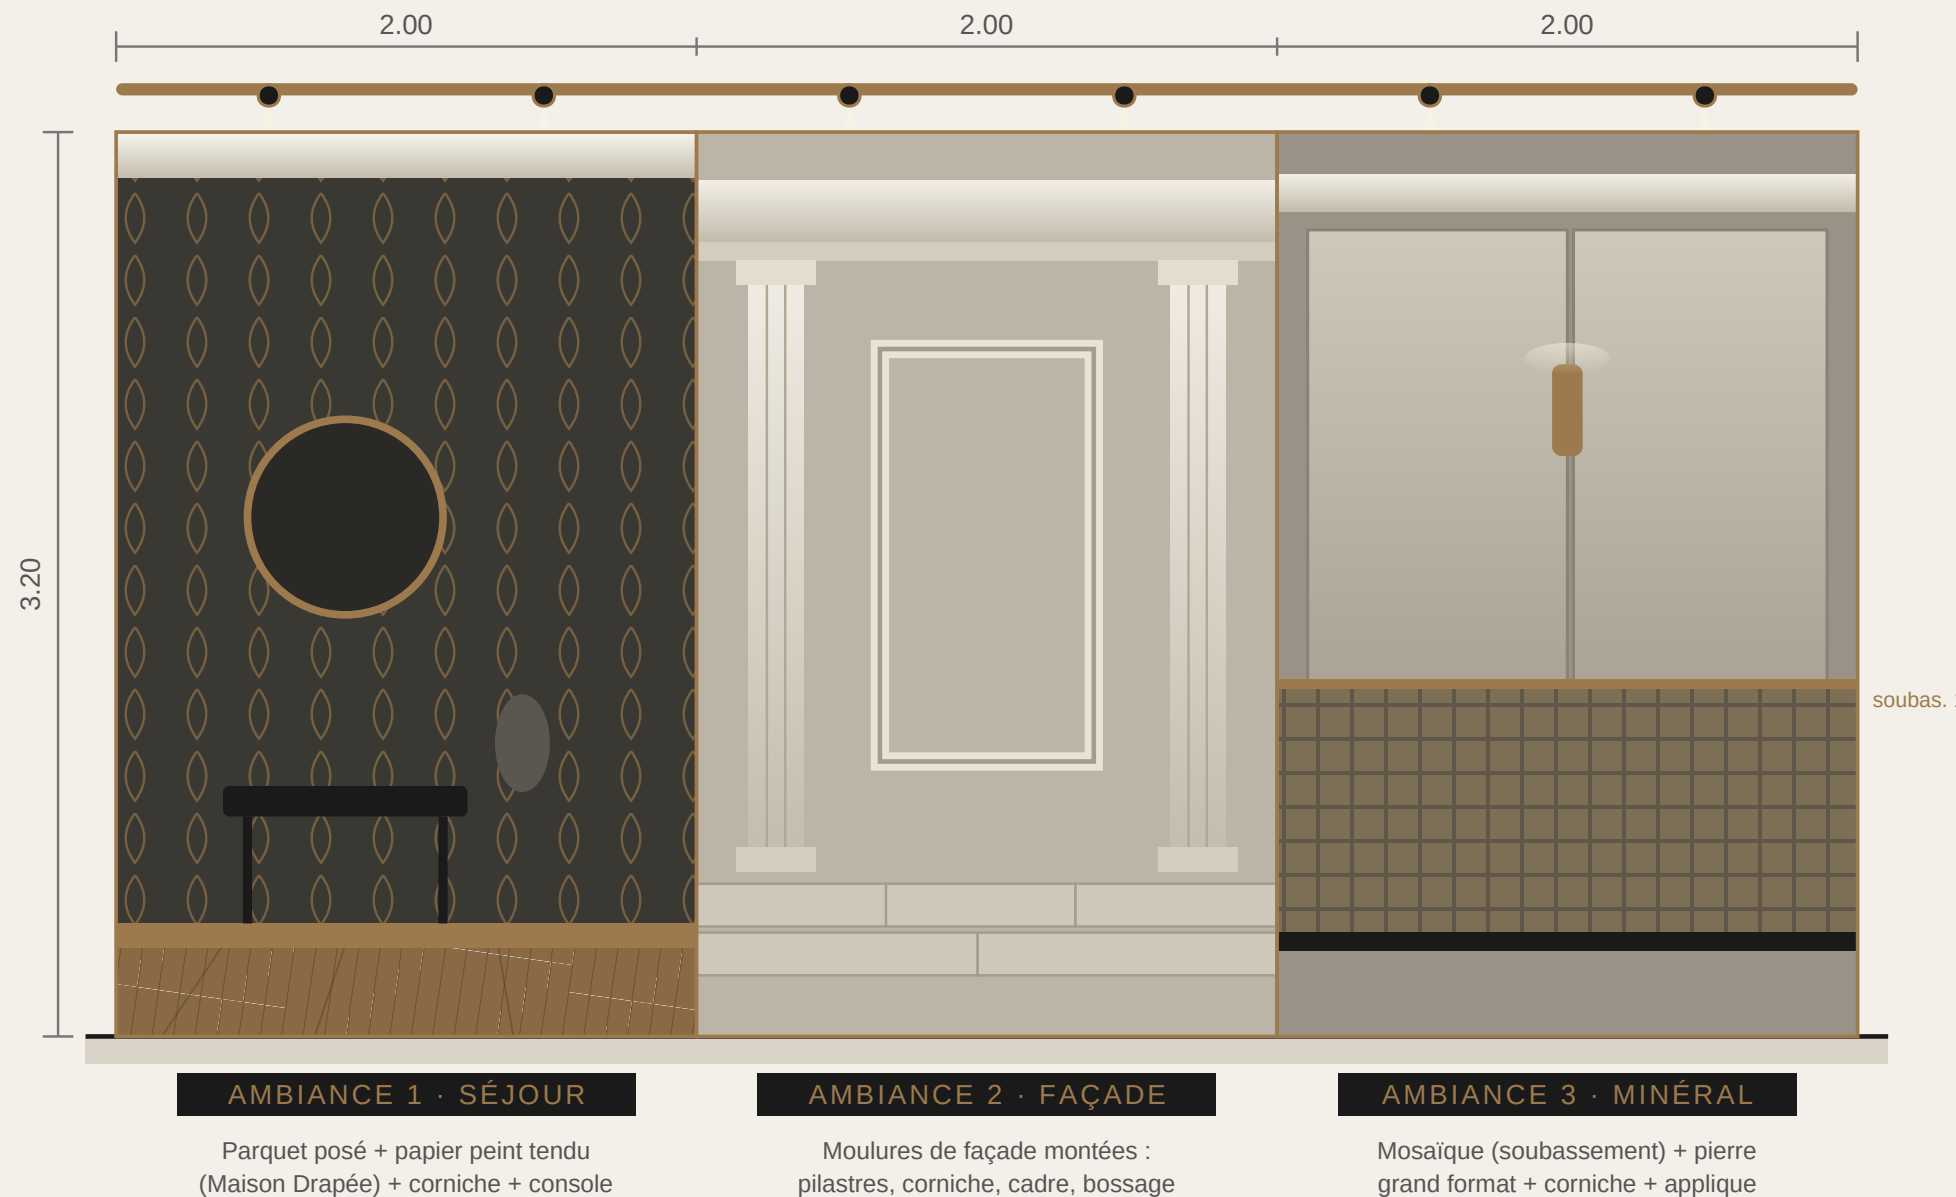

PRINCIPE DE SCÉNOGRAPHIE

- 3 niches de 2.00 m, cadrées bronze
- Produits posés "comme chez le client"
- 2 spots / niche, faisceau resserré
- Décors interchangeables (même système modulable que la matériauthèque)

PRODUITS MIS EN SCÈNE

- Séjour — papier peint + parquet
- Façade — moulures & corniches
- Minéral — mosaïque + pierre

ÉVOLUTIVITÉ

Chaque niche se re-scénographie au lancement d'une collection : on change le papier peint tendu, la moulure montée ou le calepinage mural — sans gros œuvre.

Rotation conseillée : 2×/an, ou au gré des projets phares en cours.

DARTANK · Maison Drapée — Élévation mur est (3 ambiances) — itération 1 ter

DARTANK

SHOWROOM — VUE PERSPECTIVE D'AMBIANCE

DEPUIS L'ENTRÉE VERS L'ESPACE PRESCRIPTION

perspective 1 point de fuite



DARTANK · Maison Drapée — Vue perspective — iteration 2

Gauche — Matériauthèque : panneaux modulables & tablette de consultation

Droite — Ambiances scénarisées (papier peint Maison Drapée, moulures de façade)

Fond — Espace prescription : table 4 pers. + écran catalogue digital


Plafond — Rails de spots orientables, accentuation chaude sur les échantillons

DARTANK

CONCEPT D'ÉCLAIRAGE — PLAN DE PLAFOND

VALORISATION DES ÉCHANTILLONS

2700–3000 K · IRC > 90 · éch. ≈ 1:82

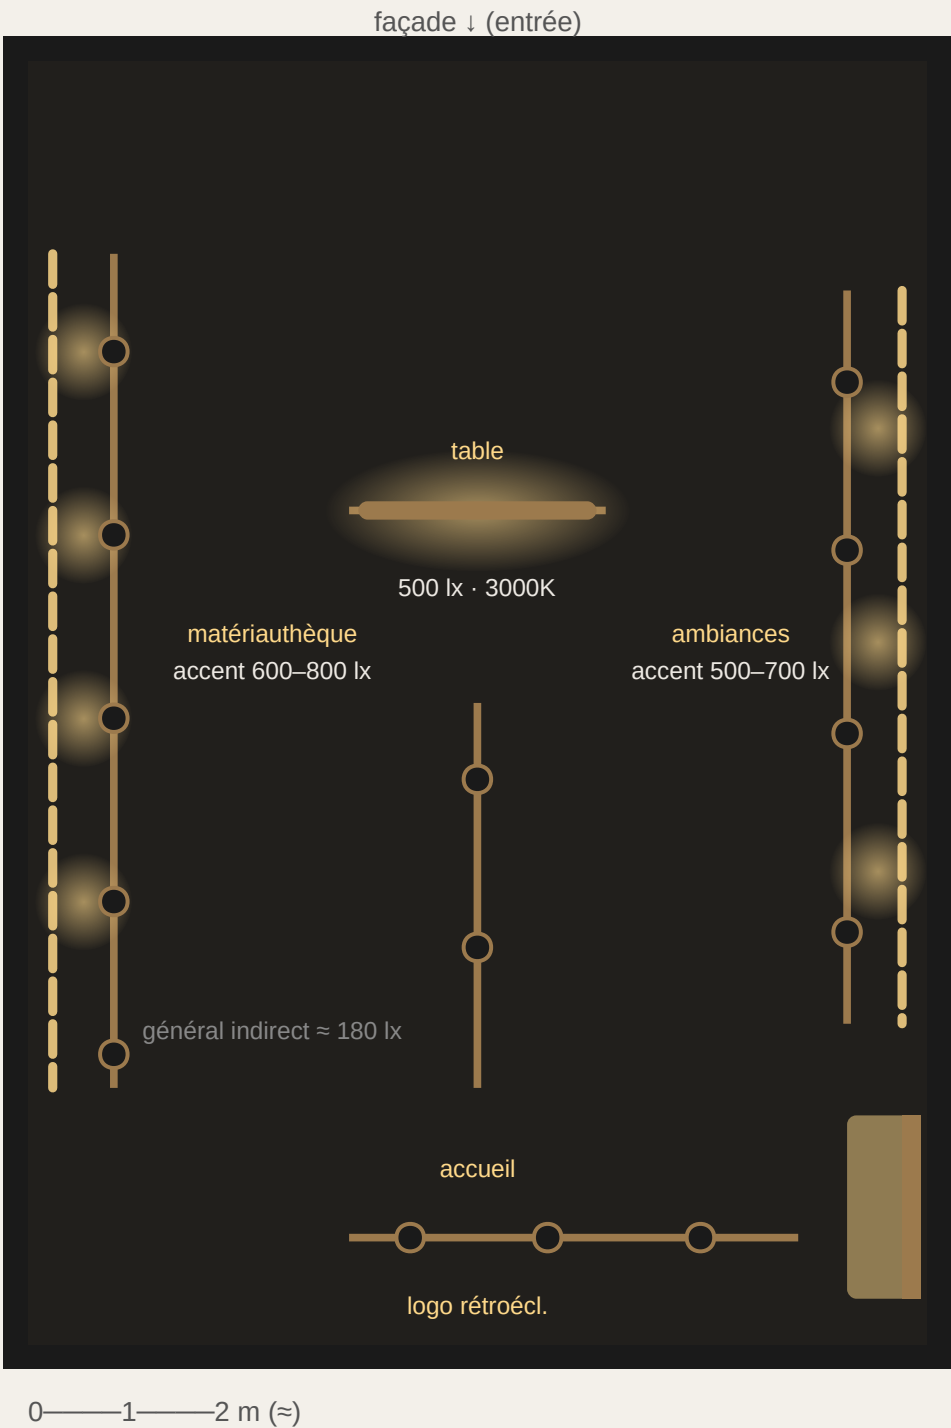

APPAREILS

- Spot orientable sur rail — LED 9W, faisceau 24°, accentuation échantillons
- Ligne LED linéaire en corniche/valance — général indirect, anti-éblouissement
- Suspension linéaire au-dessus de la table de prescription — 500 lx
- Rétroéclairage halo — mur signature & enseigne (logo DARTANK)
- Wall-grazing — lèche-mur sur les ambiances scénarisées

PARAMÈTRES CLÉS

Température	2700–3000 K (blanc chaud)	Général	150–200 lx
Rendu des couleurs	IRC > 90 — fidélité matière	Accent échantillons	600–800 lx (×4)

SCÉNARIOS (gradation DALI)

1 · ACCUEIL (jour)

Général 100% · accents 50% · logo allumé — espace lumineux & ouvert

2 · PRESCRIPTION

Table 500 lx · accents échantillons 100% · général 60% — comparaison fidèle

3 · ÉVÉNEMENT (soir)

Général tamisé 25% · accents + wall-grazing 100% · halo logo — atmosphère dramatique

4 · VITRINE (nuit)

Mur signature + 1 ambiance vitrine allumés — visibilité façade hors ouverture


□ Pilotage centralisé, 4 ambiances mémorisées · rails alimentés permettant l'ajout de spots sans intervention électrique — évolutif comme les présentoirs.

DARTANK

MATÉRIAUX & FINITIONS — MOOD BOARD


PALETTE PREMIUM · LIGNES ÉPURÉES

matériaux nobles · accent bronze/laiton

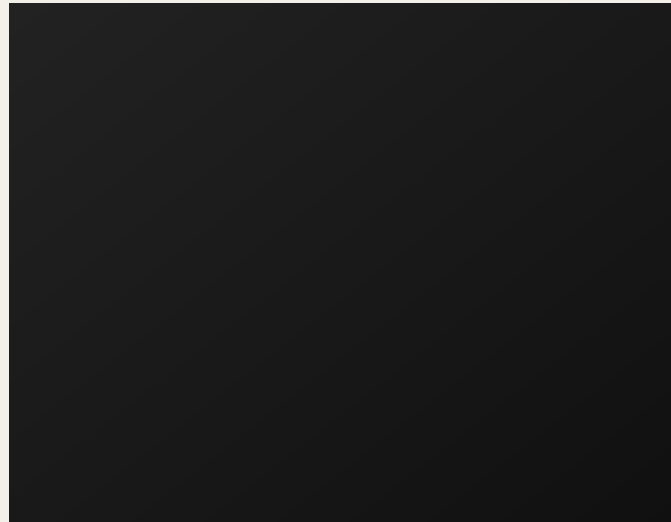

Anthracite profond #1A1A1A

Microciment / peinture mate — murs, mobilier, signature

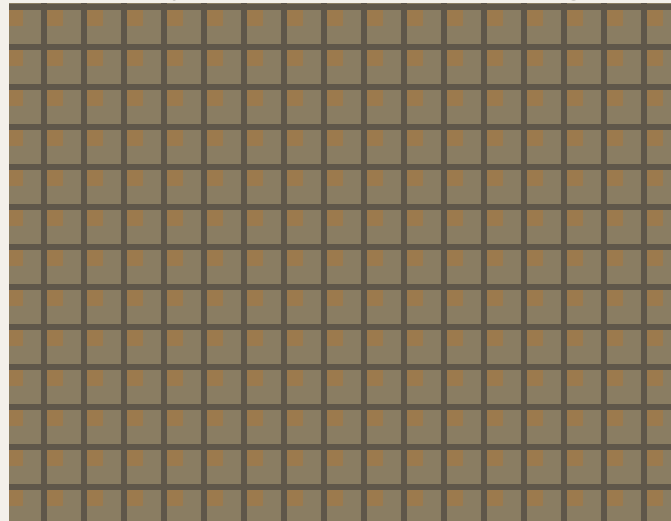

Mosaïque pierre & or accent

Touches ponctuelles, soubassements d'ambiance



Bronze / laiton brossé #9C7A4D

Détails, lettrage, mains courantes, piétements, rails



Papier peint Maison Drapée

Ambiance séjour — lés tendus, textile mural




Pierre claire #EAE5DD

Sol showroom, tablettes — respiration claire



Velours vert profond #2E3A35

Assise d'appoint / rappel coloré chic

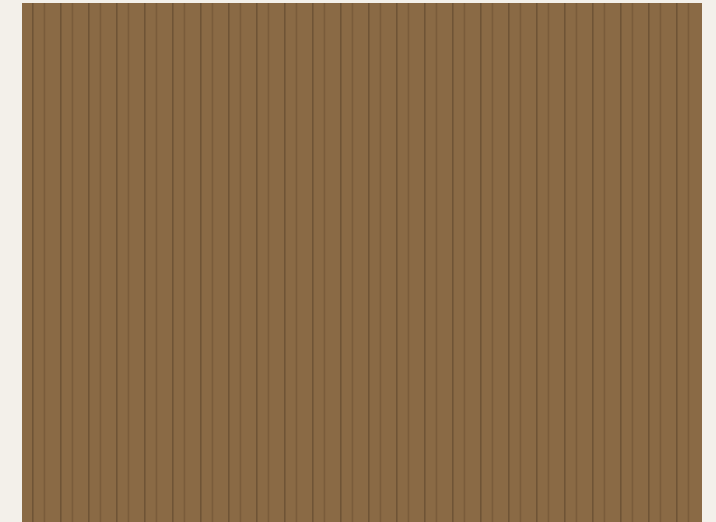

Chêne fumé sol / mobilier


Assises, plateau de table, plinthes — chaleur



Verre & miroir fumé

Cloisons, vitrine, jeux de reflets & profondeur

PALETTE

 

Anthracite
#1A1A1A




Bronze
#9C7A4D



Pierre
#EAE5DD



Taupe
#5A5650

 

Vert prof.
#2E3A35



Chêne
#8A6A45

PRINCIPES D'ASSOCIATION

- 80% neutres (anthracite + pierre), 15% bois, 5% bronze en touches — la matière exposée prime.
- Mat contre brillant : fonds mats, accents métalliques brossés & reflets de verre.
- Finitions tactiles — un showroom où l'on touche.

DARTANK

SIGNALÉTIQUE & LOGO — IDENTITÉ DE MARQUE

ENSEIGNE FAÇADE + MUR SIGNATURE

emblème portail · logotype · endossement

LOGO PRINCIPAL



DARTANK

DÉCORATION ARCHITECTURALE

ENSEIGNE DE FAÇADE — LETTRES BOÎTIER LAITON, RÉTROÉCLAIRAGE HALO



DARTANK

entrée

MUR D'ACCUEIL — LETTRES BRONZE BROSSÉ + HALO




DARTANK

DÉCORATION ARCHITECTURALE

— en collaboration avec —
Maison Drapée

VERSION CLAIRE & ENDOSSEMENT

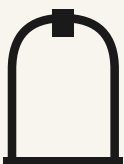

DARTANK

DÉCORATION ARCHITECTURALE

marque sœur · papiers peints

Maison Drapée

PLAQUES DE ZONE — BRONZE SUR ANTHRACITE

01 · SOLS

02 · MOULURES

03 · MOSAÏQUES

04 · PAPIERS P.

PRESCRIPTION / CONSULTATION

Plaquettes gravées laiton, fixation aimantée — repositionnables.
Pictogrammes minimalistes, même langage que l'étiquetage produit.
Numérotation = renvoi au plan & au catalogue digital.

TYPOGRAPHIE & CONSTRUCTION

- Logotype : capitales, linéale élégante, interlettrage large (≈ +10%)
 - Emblème "portail" = évocation moulure / façade architecturale
 - Endossement Maison Drapée en italique fin, jamais plus grand que DARTANK
- Zone de protection = hauteur du « D » sur tout le pourtour.

MATIÈRES & FABRICATION

- Enseigne : lettres boîtier laiton brossé, rétroéclairage halo LED 3000K
 - Mur signature : lettres relief bronze brossé sur fond microciment anthracite
 - Plaques de zone : laiton gravé, fixation aimantée (évolutif)
- Cohérence façade ↔ intérieur ↔ étiquette produit ↔ catalogue digital.

DARTANK · Maison Drapée — Signalétique & logo — itération 2