

DARTANK

D É C O R A T I O N A R C H I T E C T U R A L E

MAGASIN-SHOWROOM PREMIUM

DOSSIER D'AMÉNAGEMENT — 200 m²

PLAN · FAÇADE · PODIUMS · ROOM SETS · ÉCLAIRAGE · MATÉRIAUX · SIGNALÉTIQUE

en collaboration avec MAISON DRAPÉE — papiers peints


01	Plan d'aménagement 2D + parcours guidé 9 zones légendées · cotes · circulation · surfaces · palette	p. 3
02	Façade + vitrine Enseigne logo · vitrine produit phare · vue nuit	p. 4
03	Showroom produits — podiums par univers Sélection curatée · présentoirs modulables · renouvelables	p. 5
04	Élévations — room sets + matériauthèque Mur est (3 ambiances) · mur ouest (échantillons + catalogue digital)	p. 6
05	Vue perspective Atmosphère depuis l'entrée vers le mur signature	p. 7
06	Concept d'éclairage scénographique Plan de plafond · appareils · 2700–3000 K · IRC>90 · 4 scénarios	p. 8
07	Mood board matériaux & finitions 8 matières nobles · palette · principes d'association	p. 9
08	Signalétique, vitrine & logo DARTANK Emblème · enseigne · vitrine · mur signature · endossement Maison Drapée	p. 10

DARTANK

MAGASIN-SHOWROOM — PLAN D'AMÉNAGEMENT 2D

SÉLECTION CURATÉE · PARCOURS GUIDÉ

≈ 200 m² (12 × 17 m) · éch. ≈ 1:65 · cotes en m

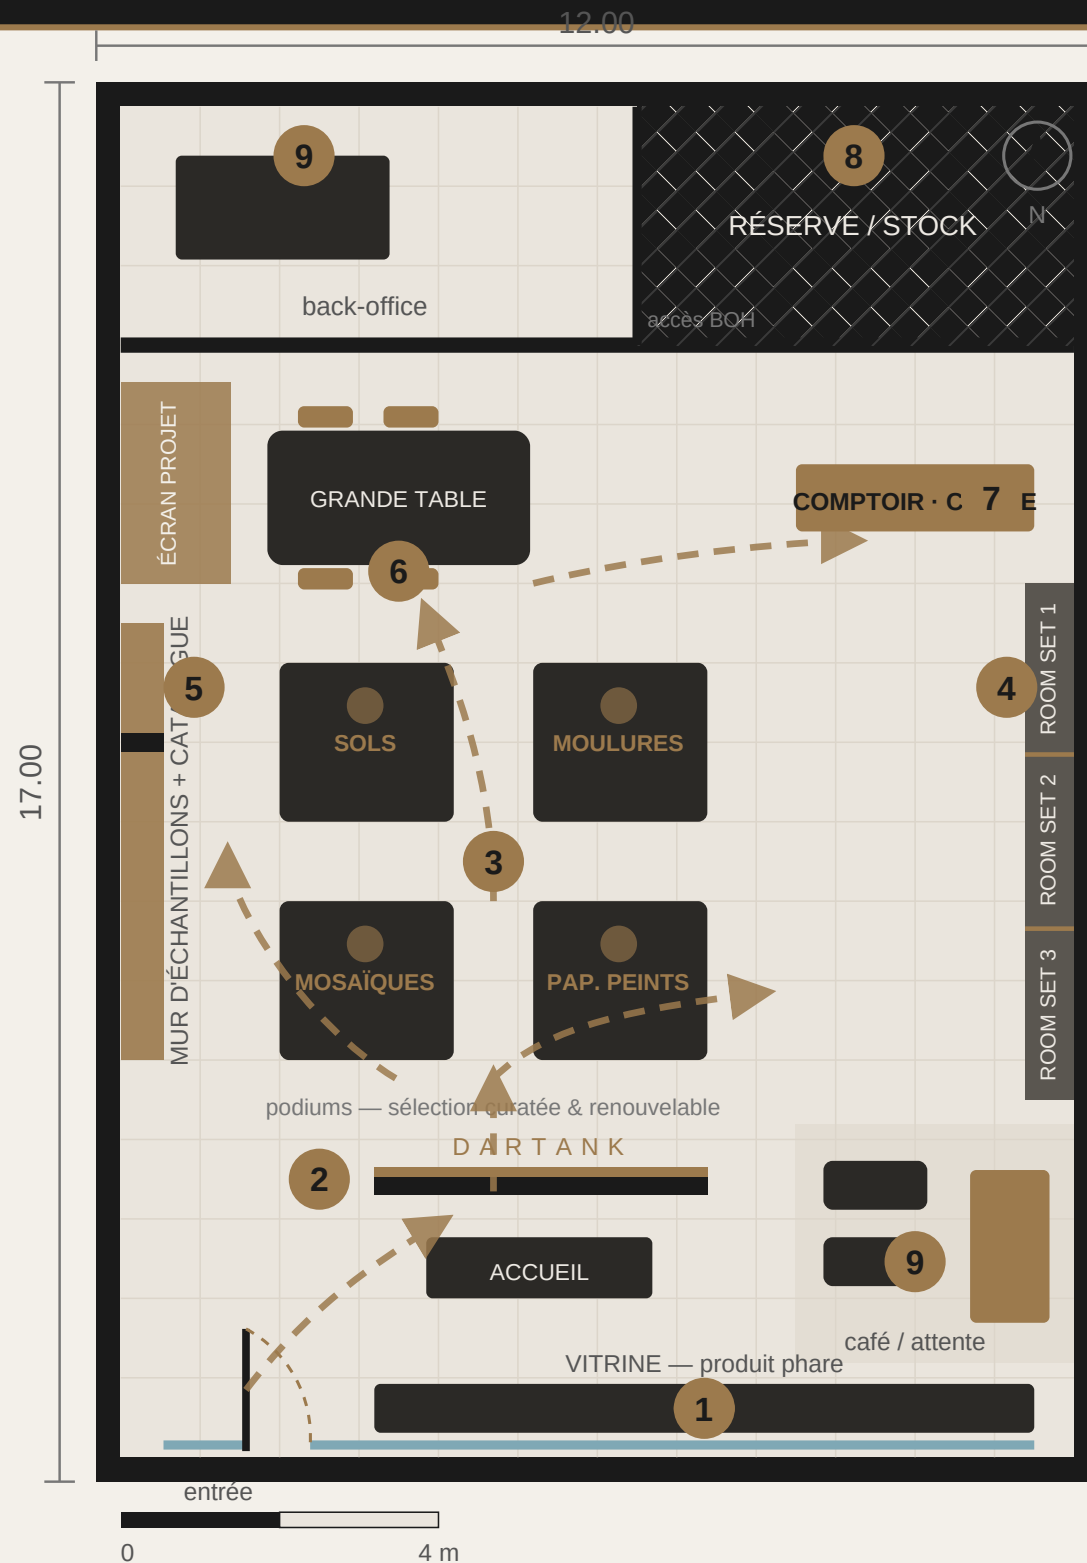


PROGRAMME

- 1 Façade · enseigne · vitrine**
Produit phare mis en scène
 - 2 Accueil + mur signature**
Logo · matière · lumière
 - 3 Showroom produits (podiums)**
Univers curatés & renouvelables
 - 4 Ambiances scénarisées x3**
Room sets en situation réelle
 - 5 Matériauthèque + catalogue digital**
Accès au reste de la gamme
 - 6 Prescription / consultation**
Grande table · écran · nuanciers
 - 7 Comptoir de vente + caisse**
 - 8 Réserve / stock**
Gammes à rotation rapide
 - 9 Back-office + café / attente**
Recevoir & patienter confortablement
- — — — — Parcours client guidé

□ Le magasin expose une sélection curatée ; le reste de la gamme est accessible via la matériauthèque + le catalogue digital (commande sur projet).

PALETTE

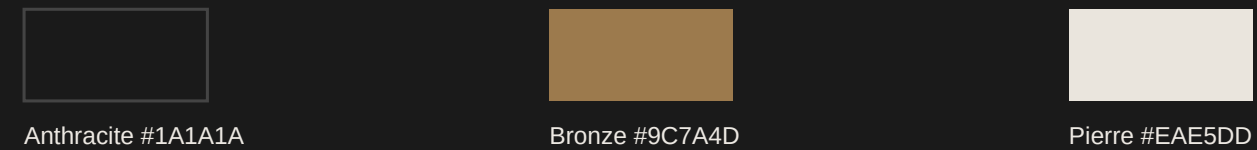

SURFACES INDICATIVES

Showroom produits + podiums	≈ 55 m ²	Café / attente	≈ 14 m ²
Ambiances scénarisées (room sets)	≈ 28 m ²	Matériauthèque + catalogue	≈ 12 m ²
Accueil + signature + vitrine	≈ 24 m ²	Back-office	≈ 12 m ²
Prescription / consultation	≈ 18 m ²	Comptoir + caisse	≈ 11 m ²
Réserve / stock	≈ 18 m ²	Circulation	≈ 8 m ²

TOTAL

≈ 200 m²

Présentoirs modulables · podiums renouvelables · rails d'éclairage évolutifs

DARTANK · Maison Drapée — Magasin-showroom 200 m² — Vue d'ensemble (itération 0)

DARTANK


FAÇADE + VITRINE — ÉLÉVATION

ENSEIGNE & MISE EN SCÈNE PRODUIT PHARE

L 12.00 × H 4.00 m · éch. ≈ 1:60




VUE DE NUIT — ENSEIGNE & VITRINE RÉTROÉCLAIRÉES

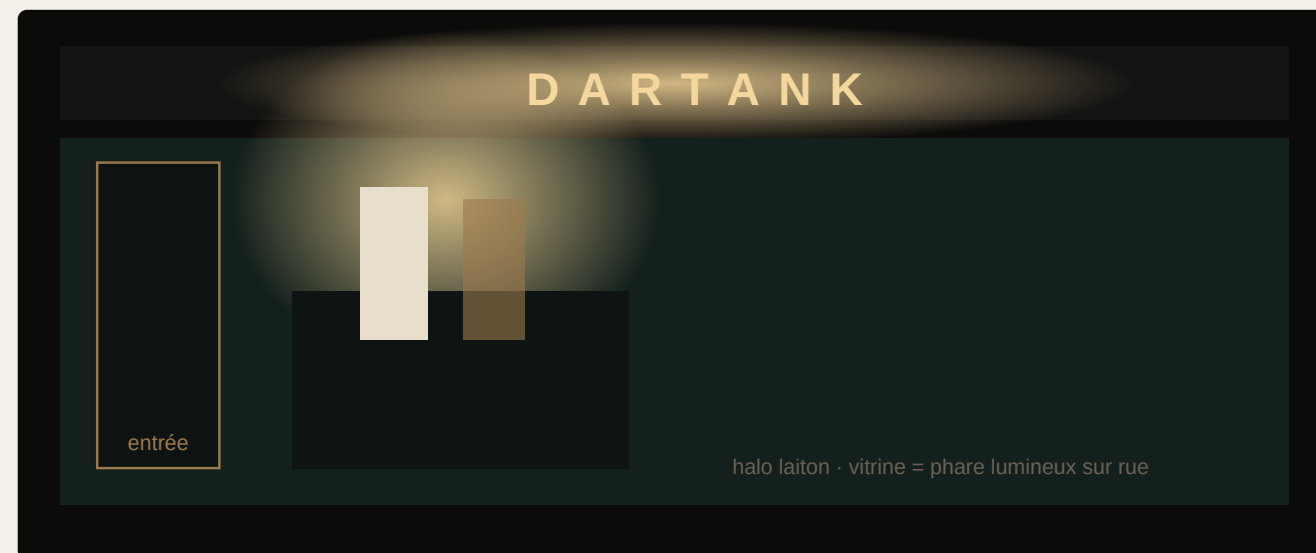

PRINCIPE & MATIÈRES

- Enseigne : lettres boîtier laiton brossé + emblème, halo LED 3000K
- Vitrine plein cintre : un seul produit phare scénarisé, podium noir mis en lumière — renouvelé à chaque collection / saison
- Châssis anthracite mat, montants fins, verre extra-clair
- Pylône latéral anthracite avec logotype vertical (repère de loin)
- Entrée vitrée à gauche, poignée bâton laiton

Objectif : lisibilité premium jour & nuit, vitrine = aimant sur rue.

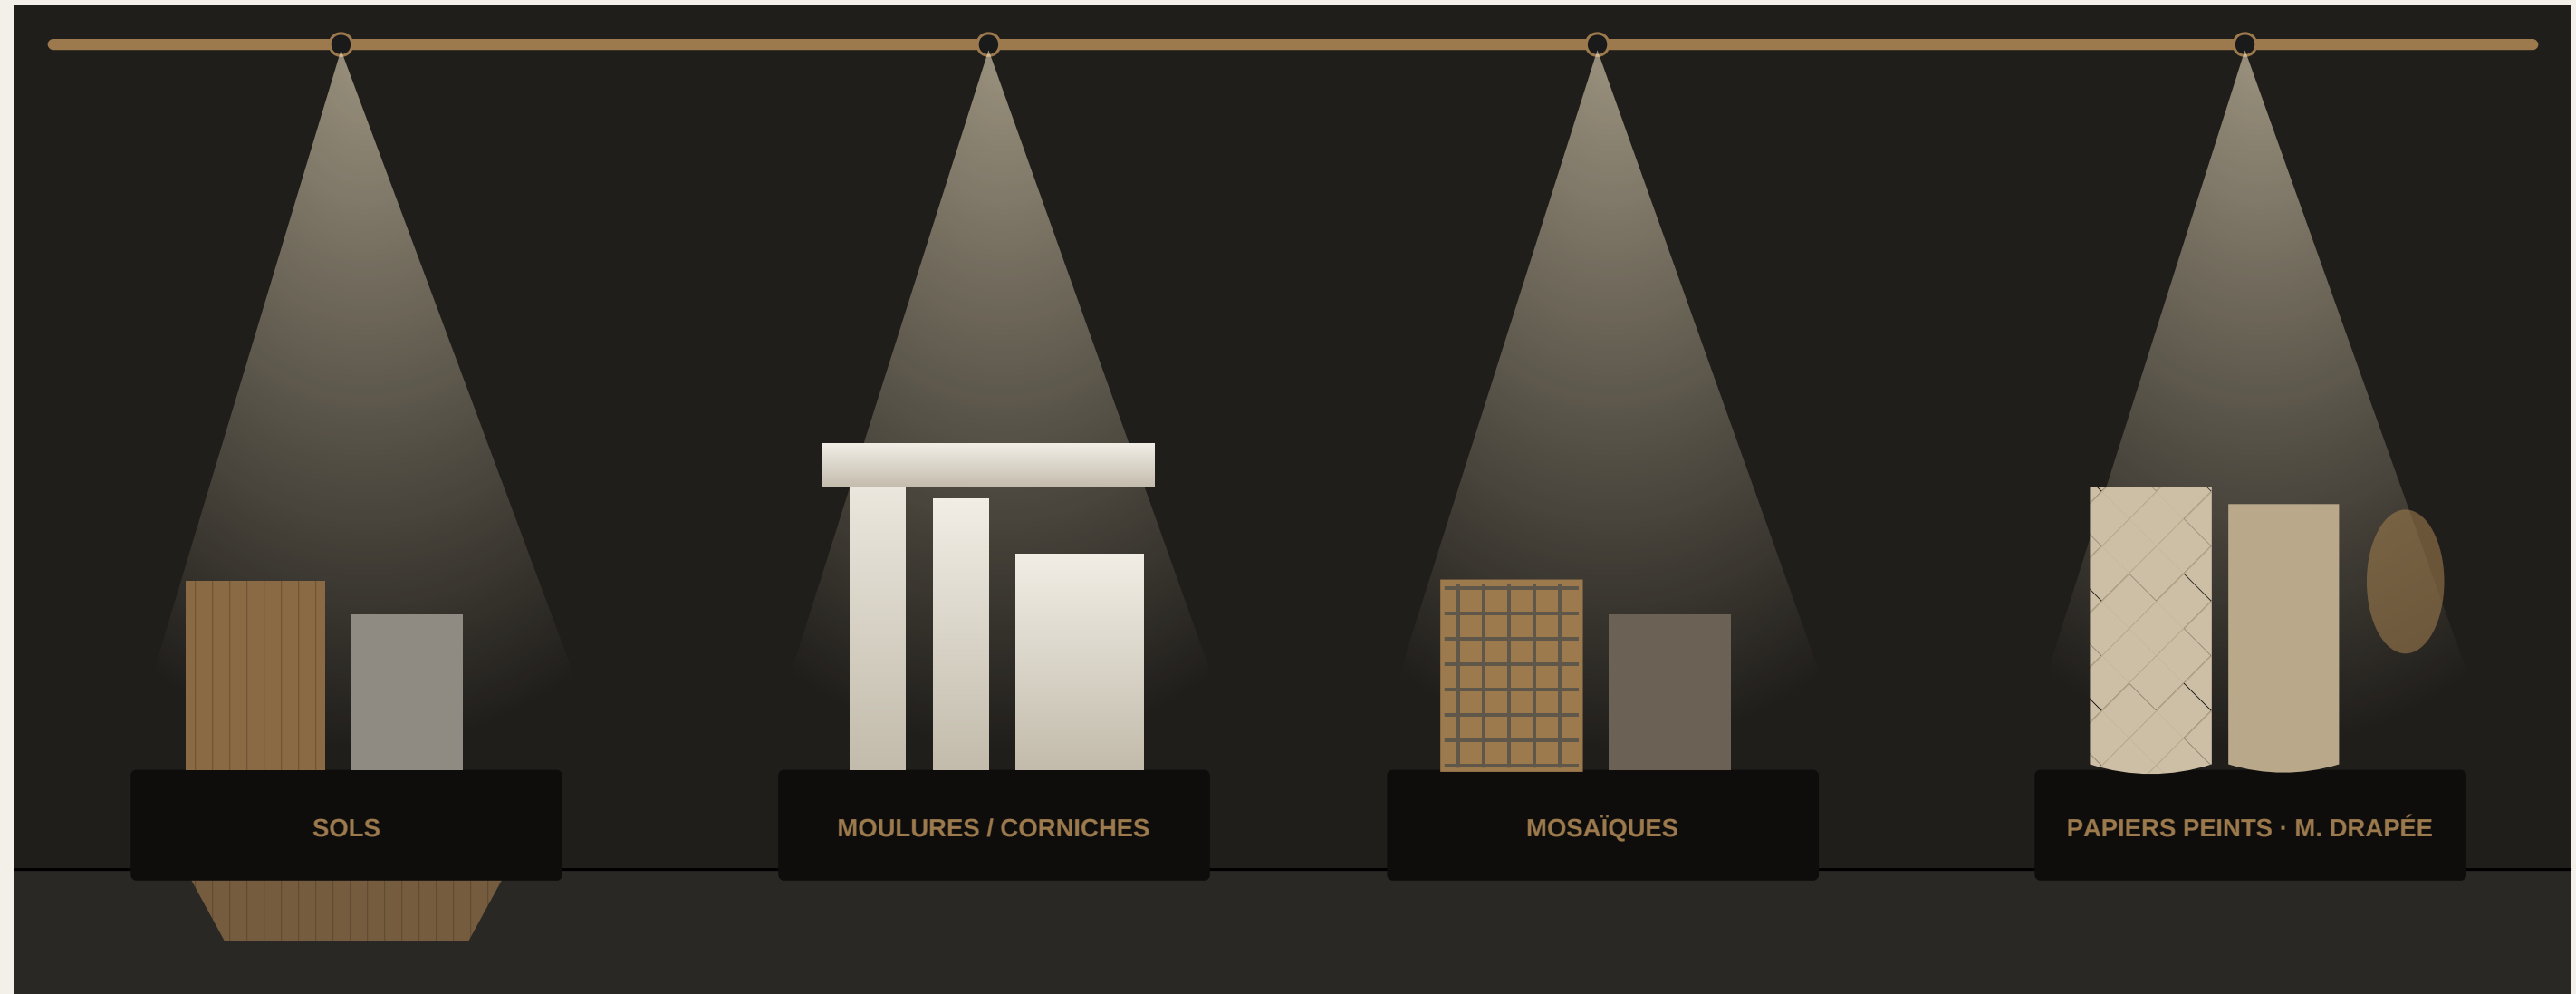


SYSTÈME DE PRÉSENTATION

- Podiums noirs mats sur fond anthracite — produit isolé, mis en lumière
- 1 podium = 1 univers ; rotation/renouvellement à chaque collection
- Présentoirs modulables : stands inclinés (sols), bras (moulures), cadres (mosaïques), barres + lest (papiers peints)
- Échantillon "à toucher" + plaquette bronze (réf. + QR catalogue)

Curaté, pas exhaustif — le reste via la matériauthèque (zone 5).

IMPLANTATION (rappel plan)

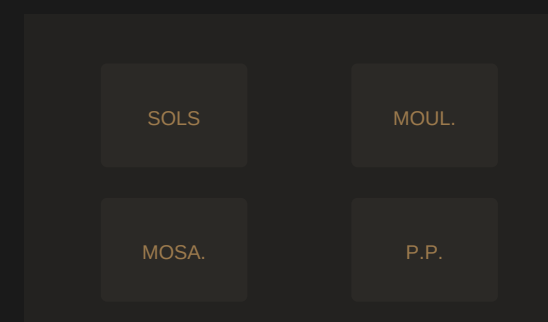

4 podiums au cœur du magasin,
circulation périphérique fluide,
vues plongeantes depuis l'entrée.

Espacement ≥ 1.2 m entre podiums
(confort & accessibilité PMR).


DARTANK

ÉLÉVATIONS — MURS PRODUITS & MATÉRIAUTHÈQUE


MUR EST (ROOM SETS) · MUR OUEST (ÉCHANTILLONS)

éch. ≈ 1:75

MUR EST — 3 AMBIANCES SCÉNARISÉES (ROOM SETS)

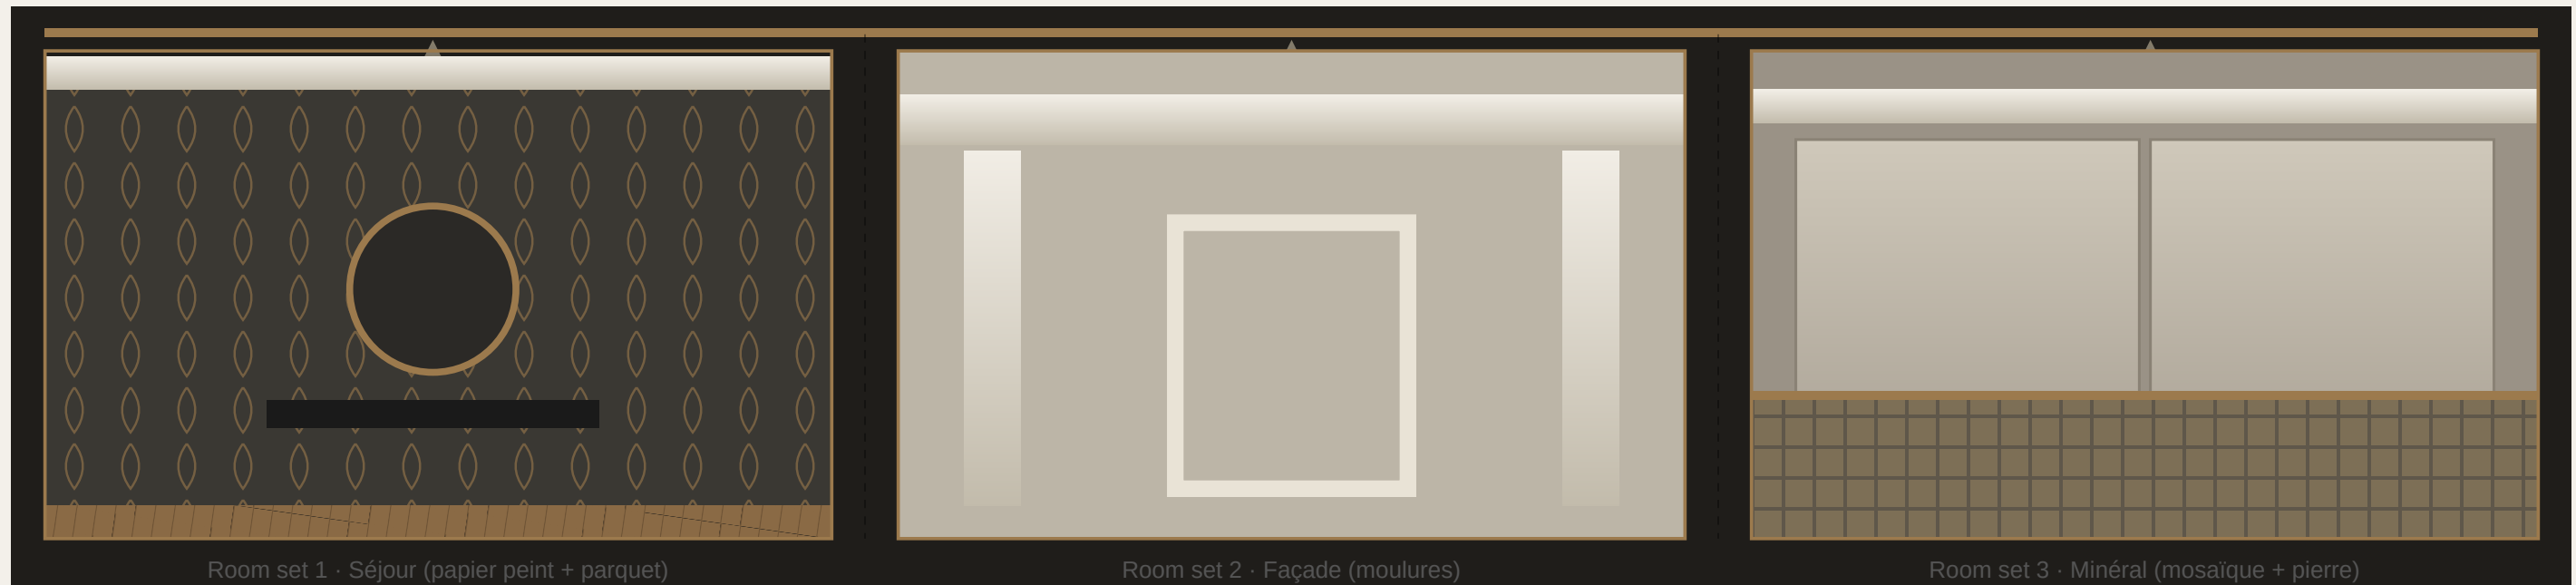

MUR OUEST — MATÉRIAUTHÈQUE (RESTE DE LA GAMME) + ÉCRAN CATALOGUE DIGITAL

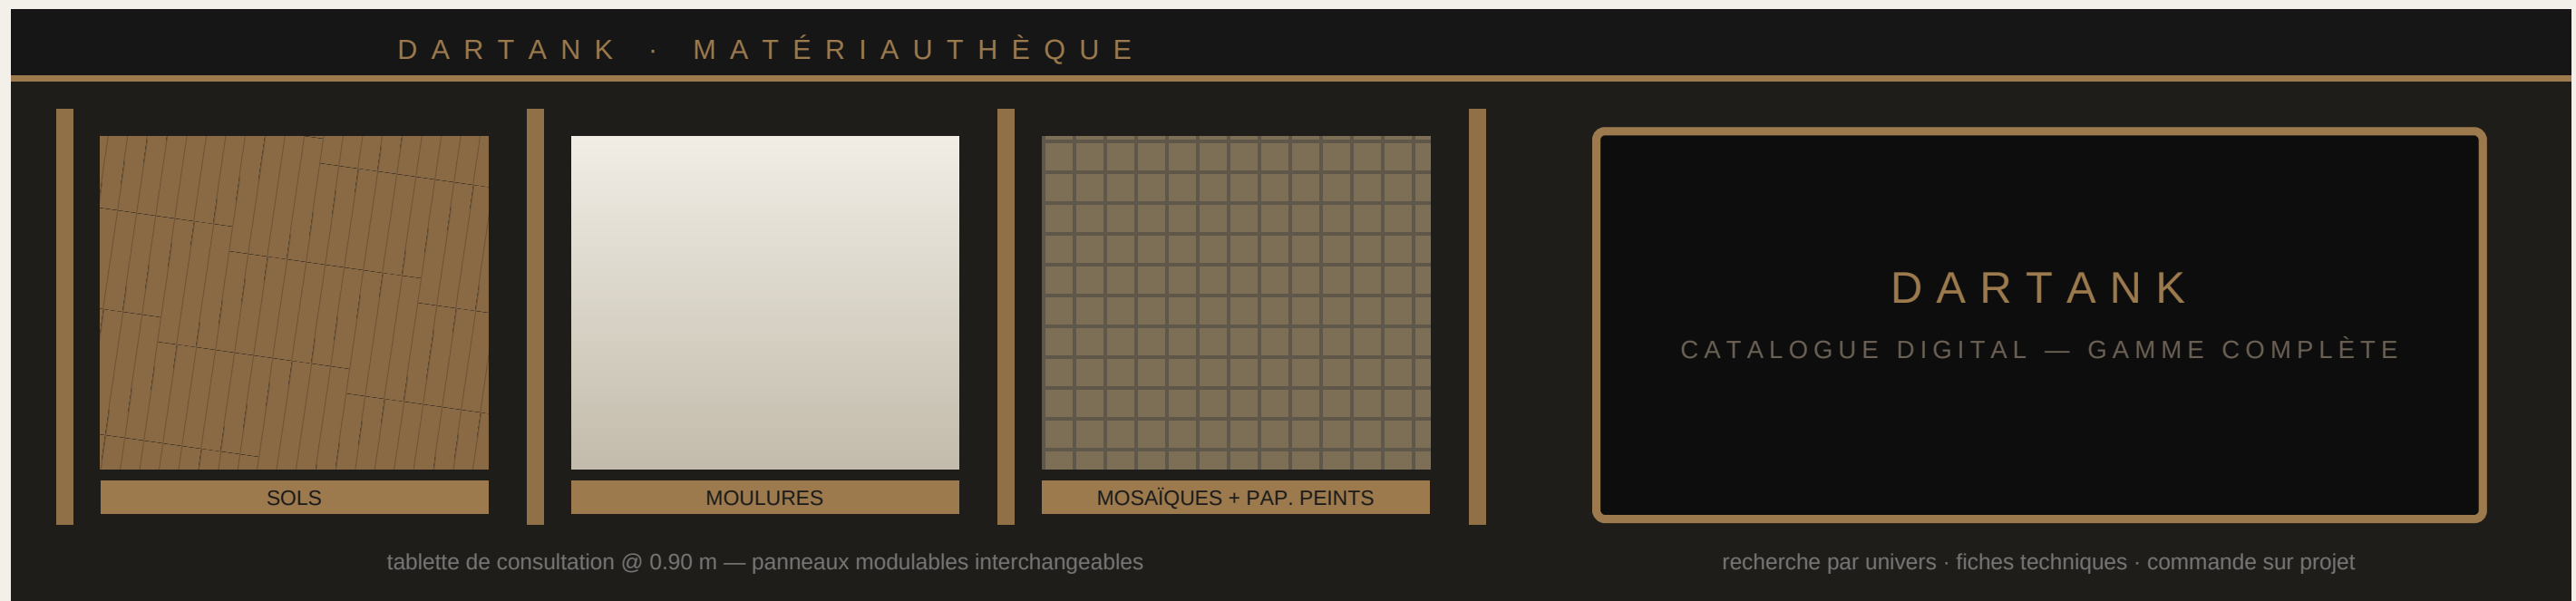

Le mur d'échantillons + l'écran donnent accès à TOUTE la gamme non exposée — sans surcharger le magasin.

DARTANK · Maison Drapée — Magasin 200 m² — Élévations murs & matériauuthèque — itération 1

DARTANK

MAGASIN — VUE PERSPECTIVE

DEPUIS L'ENTRÉE VERS LE MUR SIGNATURE

podiums & room sets sous éclairage scénographique




DARTANK · Maison Drapée — Magasin 200 m² — Perspective — iteration 1

Centre — Podiums produits par univers, isolés & mis en lumière

Gauche — Matériauthèque (reste de la gamme) + tablette de consultation

Droite — Room sets : papier peint Maison Drapée, moulures de façade

Fond — Mur signature rétroéclairé + accueil ; rails de spots scénographiques

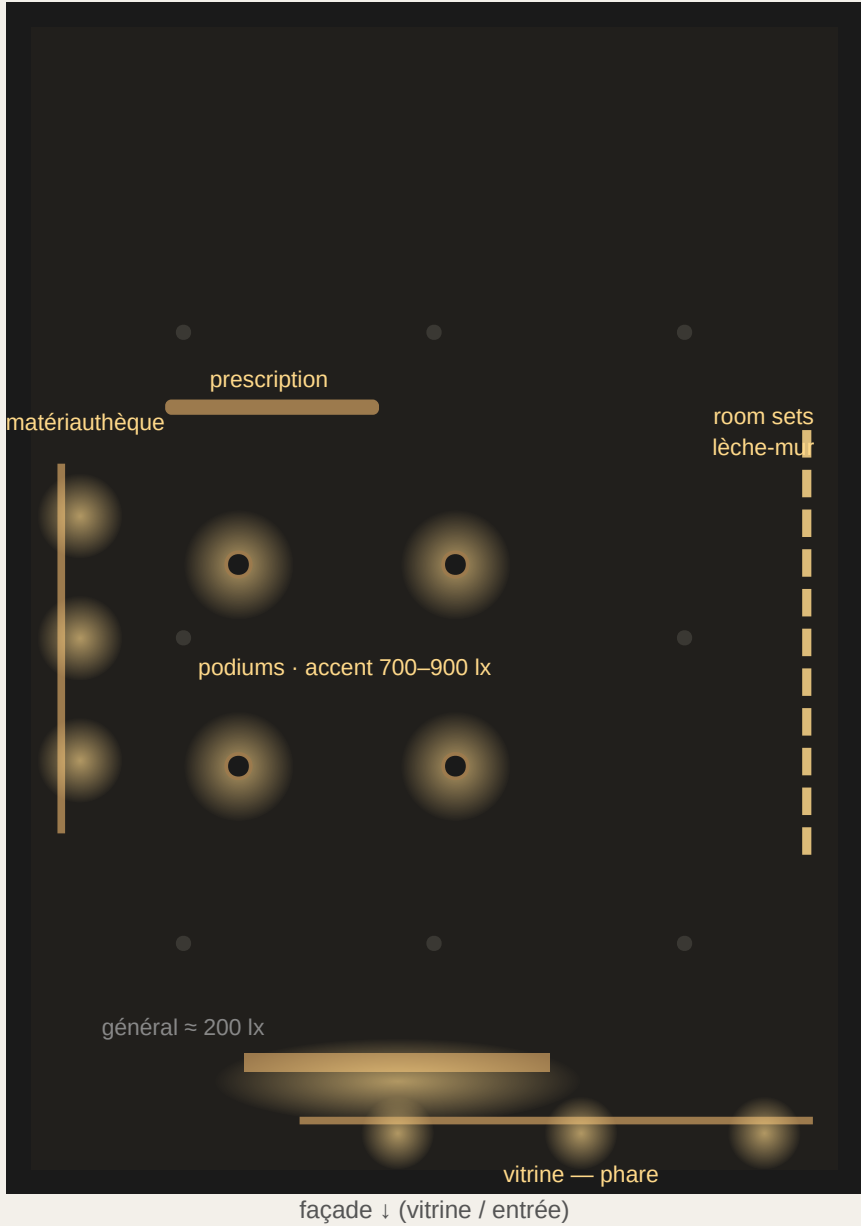

APPAREILS & PARAMÈTRES

- Spot accent sur rail — podiums & vitrine, faisceau serré 15–24°
- Lèche-mur (wall-grazing) — room sets & matériauthèque
- Downlight général encastré — circulation & confort
- Suspension linéaire — table de prescription & accueil

Température	2700–3000 K	Accent podiums	700–900 lx
Rendu couleurs (matière)	IRC > 90	Room sets	500–700 lx
Général / circulation	200 lx	Vitrine (phare)	1000 lx

Rails alimentés sur tout le plafond : ajout/déplacement de spots sans travaux — l'éclairage suit le renouvellement des podiums & des room sets.

SCÉNARIOS (gradation DALI)

1 · JOUR COMMERÇANT

Général 100% · accents podiums 80% · vitrine 100% — accueillant & lisible

2 · PRESCRIPTION (pros)

Table 500 lx · accents 100% · matériauthèque renforcée — comparaison fidèle

3 · SOIRÉE / ÉVÉNEMENT

Général 30% · accents + lèche-mur 100% · signature & vitrine — atmosphère

4 · VITRINE NUIT

Enseigne + vitrine produit phare + 1 room set allumés — présence sur rue 24/7

□ Pilotage centralisé, scénarios mémorisés, horloge astronomique pour la vitrine.


Mise en lumière = outil de merchandising : on dirige le regard vers le produit phare.

DARTANK

MATÉRIAUX & FINITIONS — MOOD BOARD


PALETTE PREMIUM · LIGNES ÉPURÉES

matériaux nobles · accent bronze/laiton

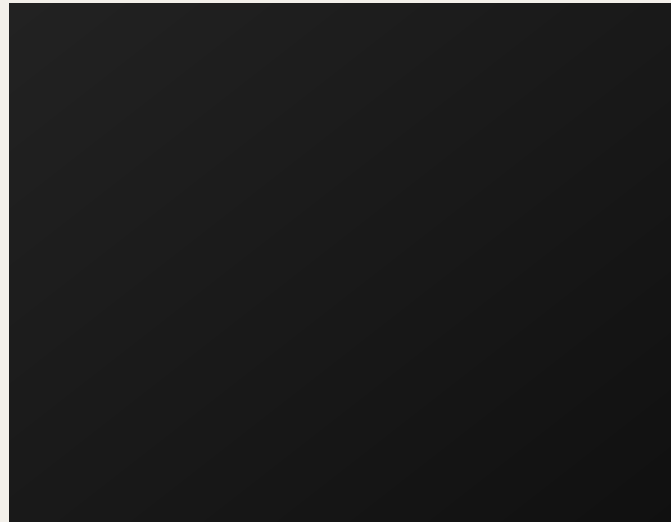

Anthracite profond #1A1A1A

Microciment / peinture mate — murs, mobilier, signature

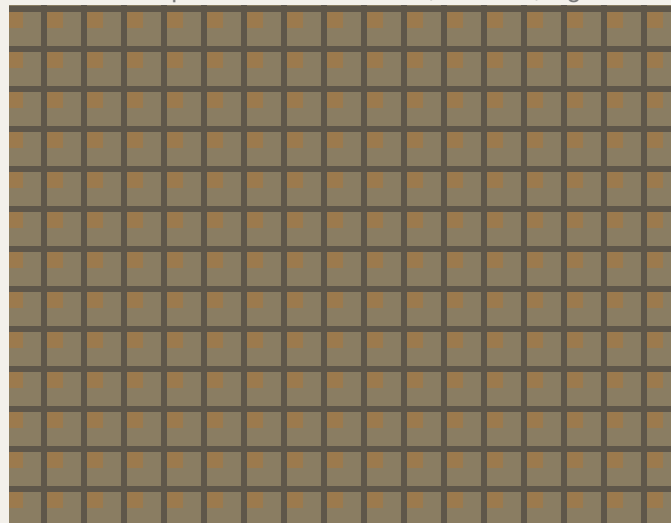

Mosaïque pierre & or accent

Touches ponctuelles, soubassements d'ambiance



Bronze / laiton brossé #9C7A4D

Détails, lettrage, mains courantes, piétements, rails



Papier peint Maison Drapée

Ambiance séjour — lés tendus, textile mural




Pierre claire #EAE5DD

Sol showroom, tablettes — respiration claire




Velours vert profond #2E3A35

Assise d'appoint / rappel coloré chic

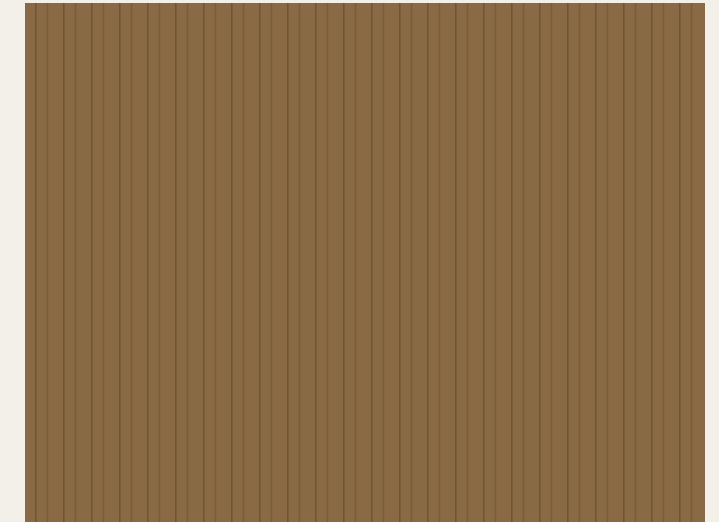

Chêne fumé sol / mobilier


Assises, plateau de table, plinthes — chaleur

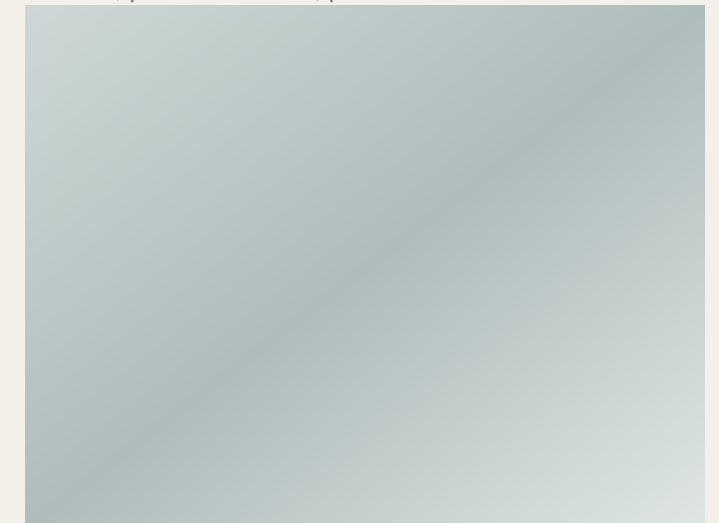

Verre & miroir fumé

Cloisons, vitrine, jeux de reflets & profondeur

PALETTE

 

Anthracite
#1A1A1A




Bronze
#9C7A4D



Pierre
#EAE5DD



Taupe
#5A5650

 

Vert prof.
#2E3A35



Chêne
#8A6A45

PRINCIPES D'ASSOCIATION

- 80% neutres (anthracite + pierre), 15% bois, 5% bronze en touches — la matière exposée prime.
- Mat contre brillant : fonds mats, accents métalliques brossés & reflets de verre.
- Finitions tactiles — un showroom où l'on touche.

DARTANK · Maison Drapée — Magasin 200 m² — Mood board matériaux & finitions — itération 1


DARTANK

SIGNALÉTIQUE, VITRINE & LOGO — IDENTITÉ DE MARQUE

ENSEIGNE · VITRINE · MUR SIGNATURE

emblème portail · logotype · endossement

LOGO PRINCIPAL

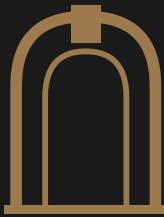

DARTANK

DÉCORATION ARCHITECTURALE

ENSEIGNE DE FAÇADE — LETTRES BOÎTIER LAITON, RÉTROÉCLAIRAGE HALO



DARTANK

entrée

MUR D'ACCUEIL — LETTRES BRONZE BROSSÉ + HALO




DARTANK

DÉCORATION ARCHITECTURALE

— en collaboration avec —
Maison Drapée

VERSION CLAIRE & ENDOSSEMENT

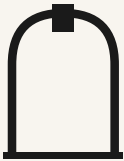

DARTANK

DÉCORATION ARCHITECTURALE

marque sœur · papiers peints

Maison Drapée

PLAQUES DE ZONE — BRONZE SUR ANTHRACITE

01 · SOLS

02 · MOULURES

03 · MOSAÏQUES

04 · PAPIERS P.

PRESCRIPTION / CONSULTATION

Plaquettes gravées laiton, fixation aimantée — repositionnables.
Pictogrammes minimalistes, même langage que l'étiquetage produit.
Numérotation = renvoi au plan & au catalogue digital.

TYPOGRAPHIE & CONSTRUCTION

- Logotype : capitales, linéale élégante, interlettrage large (≈ +10%)
 - Emblème "portail" = évocation moulure / façade architecturale
 - Endossement Maison Drapée en italique fin, jamais plus grand que DARTANK
- Zone de protection = hauteur du « D » sur tout le pourtour.

MATIÈRES & FABRICATION

- Enseigne : lettres boîtier laiton brossé, rétroéclairage halo LED 3000K
 - Mur signature : lettres relief bronze brossé sur fond microciment anthracite
 - Vitrine : logo & mention dépolis / sérigraphiés sur verre, lettrage laiton
- Cohérence façade ↔ vitrine ↔ intérieur ↔ étiquette produit ↔ catalogue digital.

DARTANK · Maison Drapée — Magasin 200 m² — Signalétique, vitrine & logo — itération 1